SCALE: 1" = 60'

SHEET 1 OF FOUR SHEETS

TRACT Nº 11569

IN THE CITY OF LOS ANGELES

BEING A SUBDIVISION OF A PORTION OF RANCHO AGUAJE DE LA CENTINELLA, AS PER MAP RECORDED IN PATENT BOOK 1, PAGE 512, RECORDS OF LOS ANGELES COUNTY.

RECORDED
AT REQUEST OF OWNER
May 22, 1947
31 MIN. PAST 2 P.M.
IN BOOK 303
AT PAGE 17
OF MAP RECORDS
LOS ANGELES COUNTY, CALIF.
MAME B. BEATTY,
County Recorder
By B.M. Woodbury Deputy
$5.00

SEABOARD ENGINEERING CO.

MARK A. ROBIN, REGISTERED CIVIL ENGINEER Nº 2059

BASIS OF BEARINGS

THE BEARING N. 43° 08' 34" E. OF THE CENTER LINE OF LA TIJERA BOULEVARD, SHOWN AS N. 43° 15' 10" E. ON COUNTY SURVEYORS MAP, C. S. B. 310-6, WAS TAKEN AS THE BASIS OF BEARINGS SHOWN ON THIS MAP.

We hereby certify that we are the owners of, or are interested in the lands included within the subdivision shown on this map within the colored border lines, and we consent to the preparation and recordation of said map and subdivision; and we hereby dedicate to the public use all streets, avenues, place, and alley shown on said map within said subdivision, and we also grant and dedicate to the City of Los Angeles perpetual easements for *drainage* and Sanitary Sewer purposes, over the strips of land so designated on said map within said subdivision.

GENERAL REALTY CO.

F. W. Marlow
President

F. D. Baillet
Secretary

LOS ANGELES INVESTMENT COMPANY

R. F. Ingold
R. F. INGOLD President

W. R. Hilker
W. R. HILKER Secretary

I, MARK A. ROBIN, hereby certify that I am a Registered Civil Engineer of the State of California, and that this map, consisting of four sheets, correctly represents a survey made under my supervision, March 1946, that the survey is true and complete as shown, that the monuments shown hereon, actually exist or will be in place not later than *August 1st 1947*, that their positions and character are correctly shown, and that said monuments are sufficient to enable the survey to be retraced.

Mark A. Robin
REGISTERED CIVIL ENGINEER, CERTIFICATE Nº 2059.

STATE OF CALIFORNIA }
COUNTY OF LOS ANGELES } ss

On this 28th day of MARCH 1947, before me ALTHEA HAGLUND a Notary Public in and for said county personally appeared F. W. MARLOW known to me to be the President, and F. D. BAILLET known to me to be the Secretary of General Realty Co., the corporation that executed the within instrument and known to me to be the persons who executed the within instrument on behalf of the corporation therein named, and acknowledged that said Corporation executed the same.

Althea Haglund
NOTARY PUBLIC IN AND FOR LOS ANGELES COUNTY, STATE OF CALIFORNIA
MY COMMISSION EXPIRES JANUARY 4th 1949.

STATE OF CALIFORNIA }
COUNTY OF LOS ANGELES } ss

On this 27th day of March 1947, before me Irma Harris a Notary Public in and for said county personally appeared R. F. INGOLD known to me to be the President, and W. R. HILKER known to me to be the Secretary of Los Angeles Investment Company the corporation that executed the within instrument and known to me to be the persons who executed the within instrument on behalf of the corporation therein named, and acknowledged that said Corporation executed the same.

Irma Harris
NOTARY PUBLIC IN AND FOR LOS ANGELES COUNTY, STATE OF CALIFORNIA

[illegible] S, STATE OF CALIFORNIA, A CERTI- [illegible] TITLE INSURANCE AND TRUST COMPANY [illegible] NO. 2433814 DATED APRIL 15 1947 [illegible] NG THAT IT APPEARS FROM THE RECORDS [illegible] ITY THAT GENERAL REALTY CO LOS ANGELES INVESTMENT COMPANY [illegible] PERSONS WHOSE CONSENT IS REQUIRED [illegible] OF THIS MAP BY LAW.

[illegible] MAY 20 1947

[illegible] OF THE CITY OF [illegible] AND ACCEPTED [illegible] ROADS, A[illegible] ON SA[illegible] OFFERED FOR [illegible] EXCEPT THOSE STRIPS MARKED "FUTURE STREET" AND "FUTURE ALLEY" PROVIDED THAT NOTHING HEREIN CONTAINED SHALL BE CONSTRUED AS AN ACCEPTANCE OF ANY IMPROVEMENTS MADE IN OR UPON ANY STREET, ROAD, ALLEY, HIGHWAY OR EASEMENT SHOWN ON THIS MAP.

DATE 5/21/1947 CITY CLERK Walter C. Peterson
by A. M. Morris
Deputy.

I HEREBY CERTIFY THAT I HAVE EXAMINED THIS MAP AND THAT THE SUBDIVISION AS SHOWN HEREON IS [illegible]

[illegible] MAY 20 47

I hereby certify that a good and sufficient bond in the sum of $ 1500.00 duly approved by the Board of Supervisors of the County of Los Angeles has been filed with said Board as security for the [illegible] special assessments collected as taxes on land shown on [illegible]
Tract No. 11569 as [illegible] by law.

J.F. Moroney, County Clerk and Ex-officio [illegible] of Supervisors of the County of Los Angeles, State of California.
By Mez Robinson Deputy

Approved May 22, 1947
ALFRED JONES, County Surveyor
By Lee H. Lucas
Deputy

I HEREBY CERTIFY THAT ALL SPECIAL ASSESSMENTS OF WHICH I AM IN CHARGE TO WHICH THE LAND INCLUDED IN THE WITHIN SUBDIVISION OR ANY PART THEREOF IS SUBJECT AND WHICH MAY BE PAID IN FULL HAVE BEEN PAID IN FULL.

DIRECTOR BUREAU OF ASSESSMENTS C. K. STEELE
DATE 4/14 1947 DEPUTY G. Hitchens

SCALE: 1" = 60'

SHEET 2 OF FOUR SHEETS

TRACT No 11569

RECORDED
AT REQUEST OF OWNER
May 22, 1947
31 MIN. PAST 2 P.M.
IN BOOK 303
AT PAGE 18
OF MAP RECORDS
LOS ANGELES COUNTY, CALIF.
MAME B. BEATTY
County Recorder
By E. M. Woodbury Deputy
Free

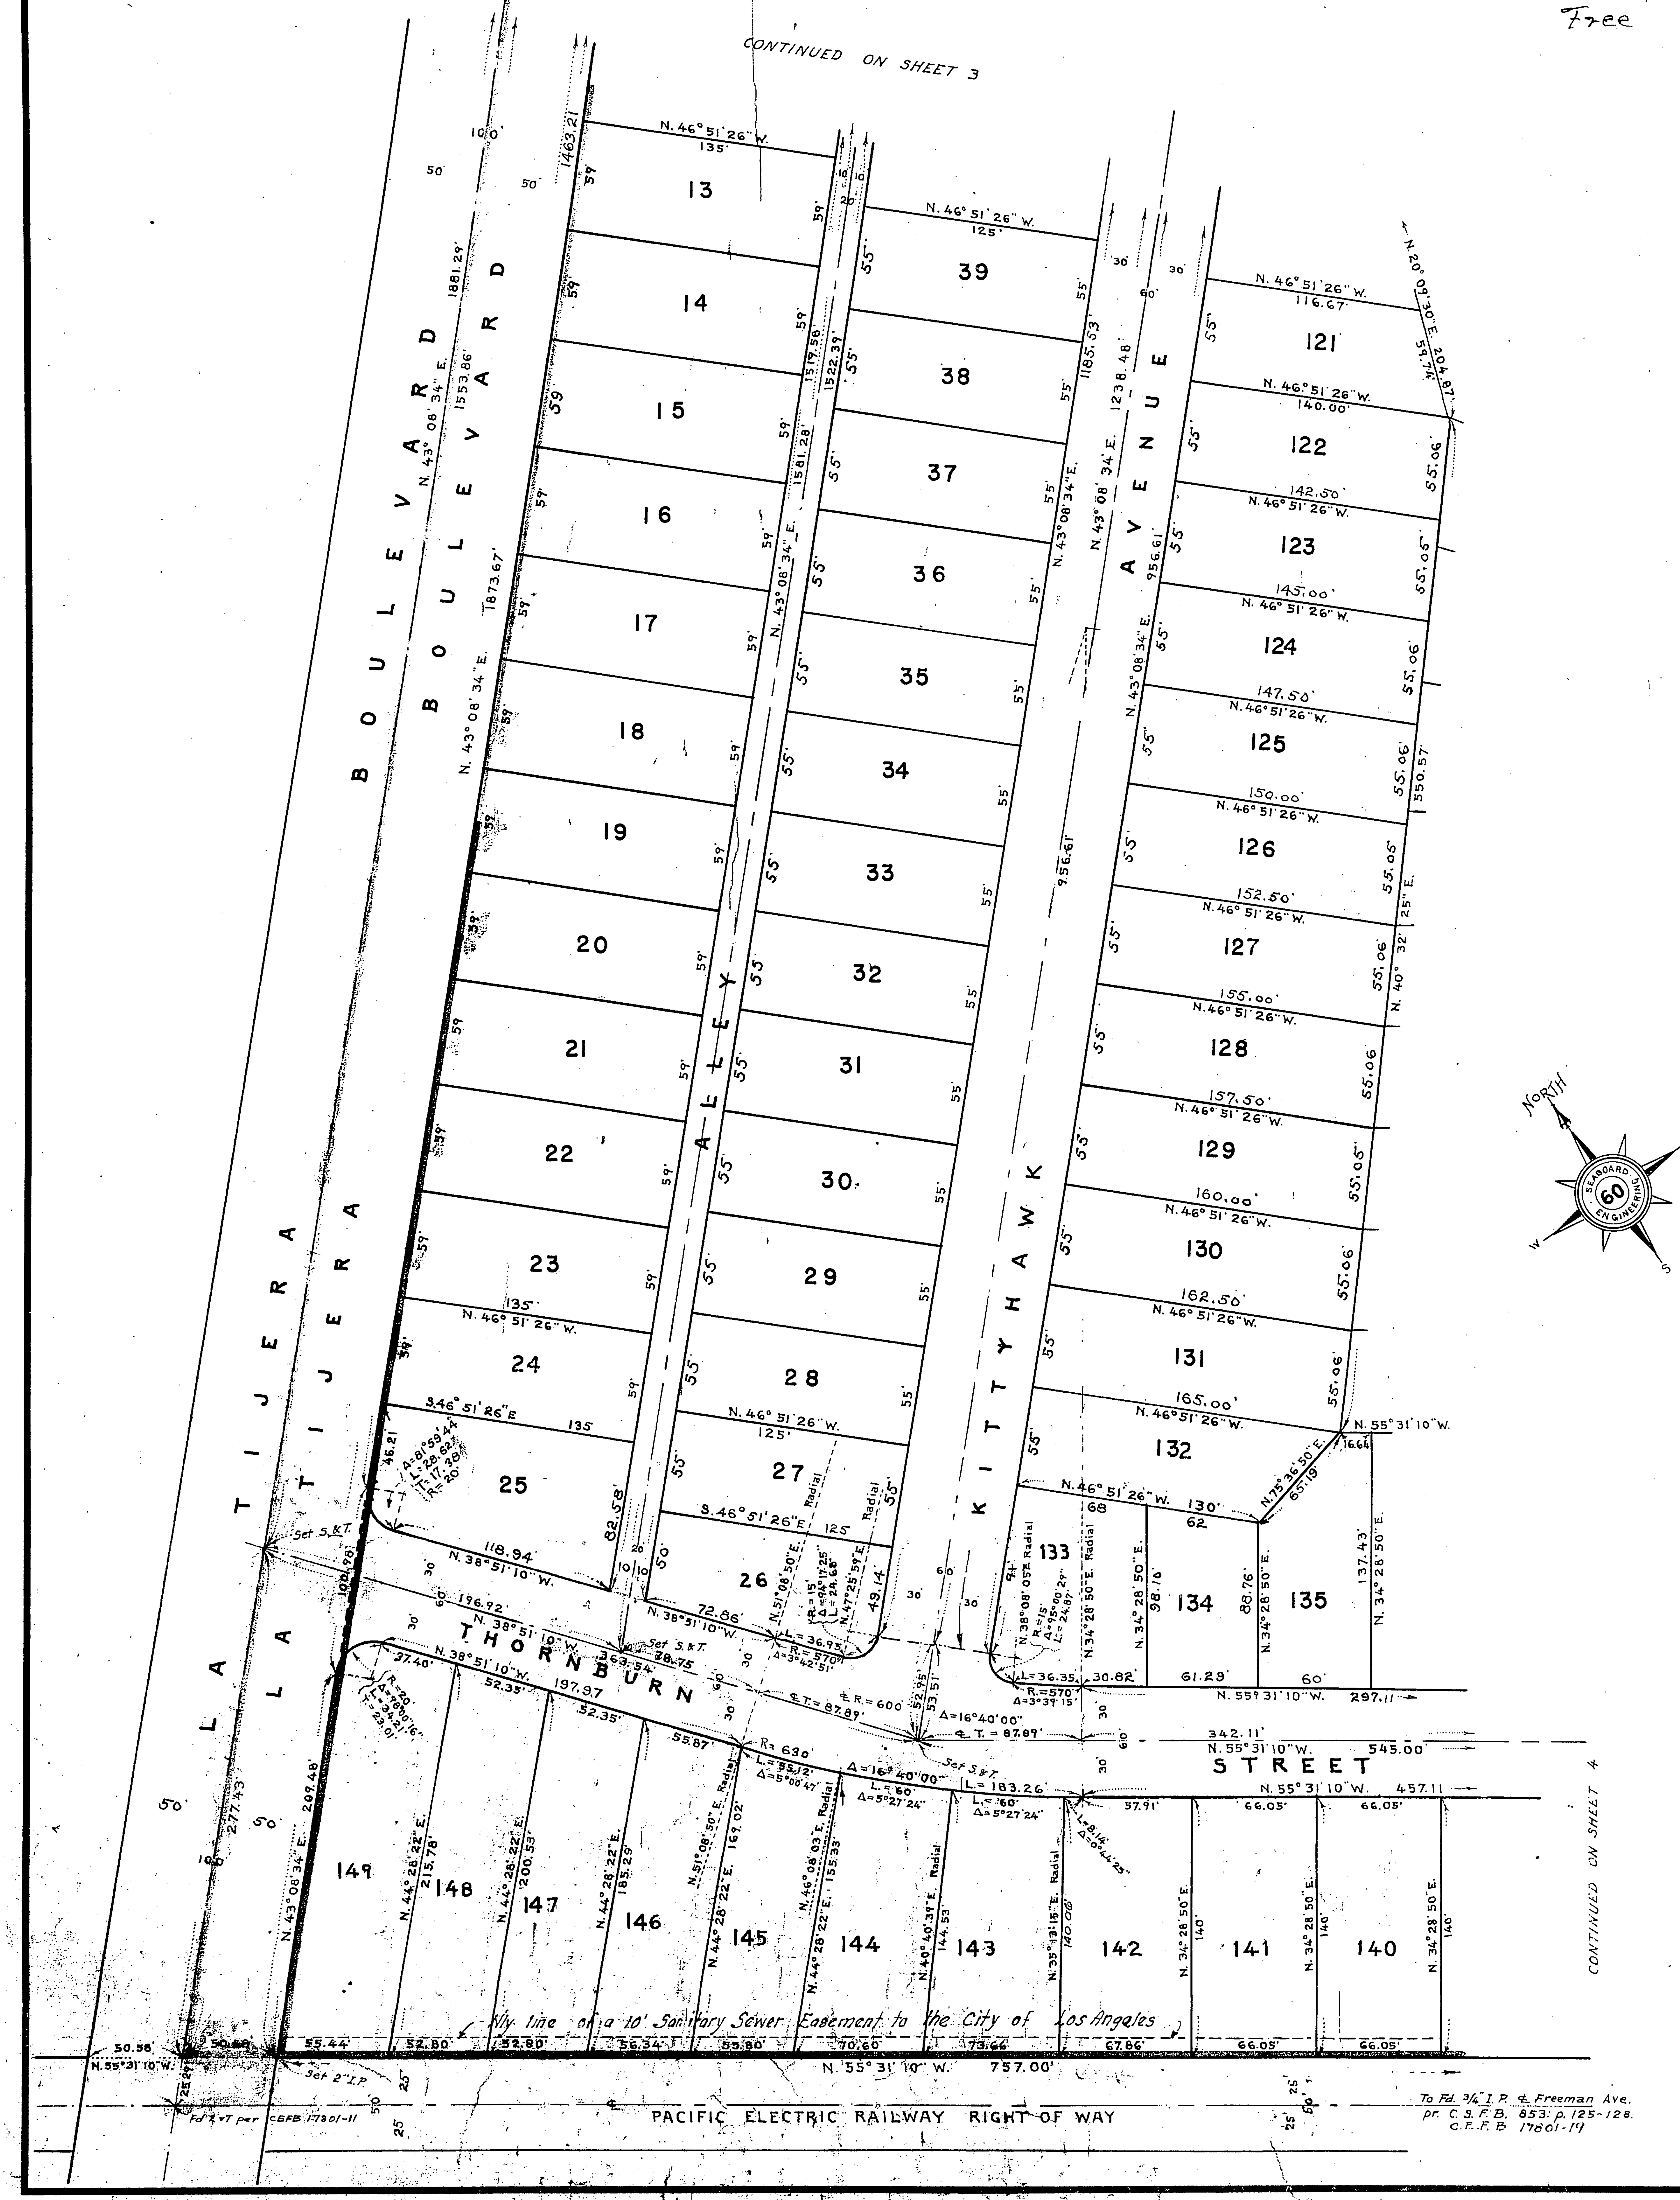

SCALE: 1" = 60'

SHEET 3 OF FOUR SHEETS

TRACT No 11569

May 22, 1947
31 2 P.M.
303
19

W. M. Woodbury
Free

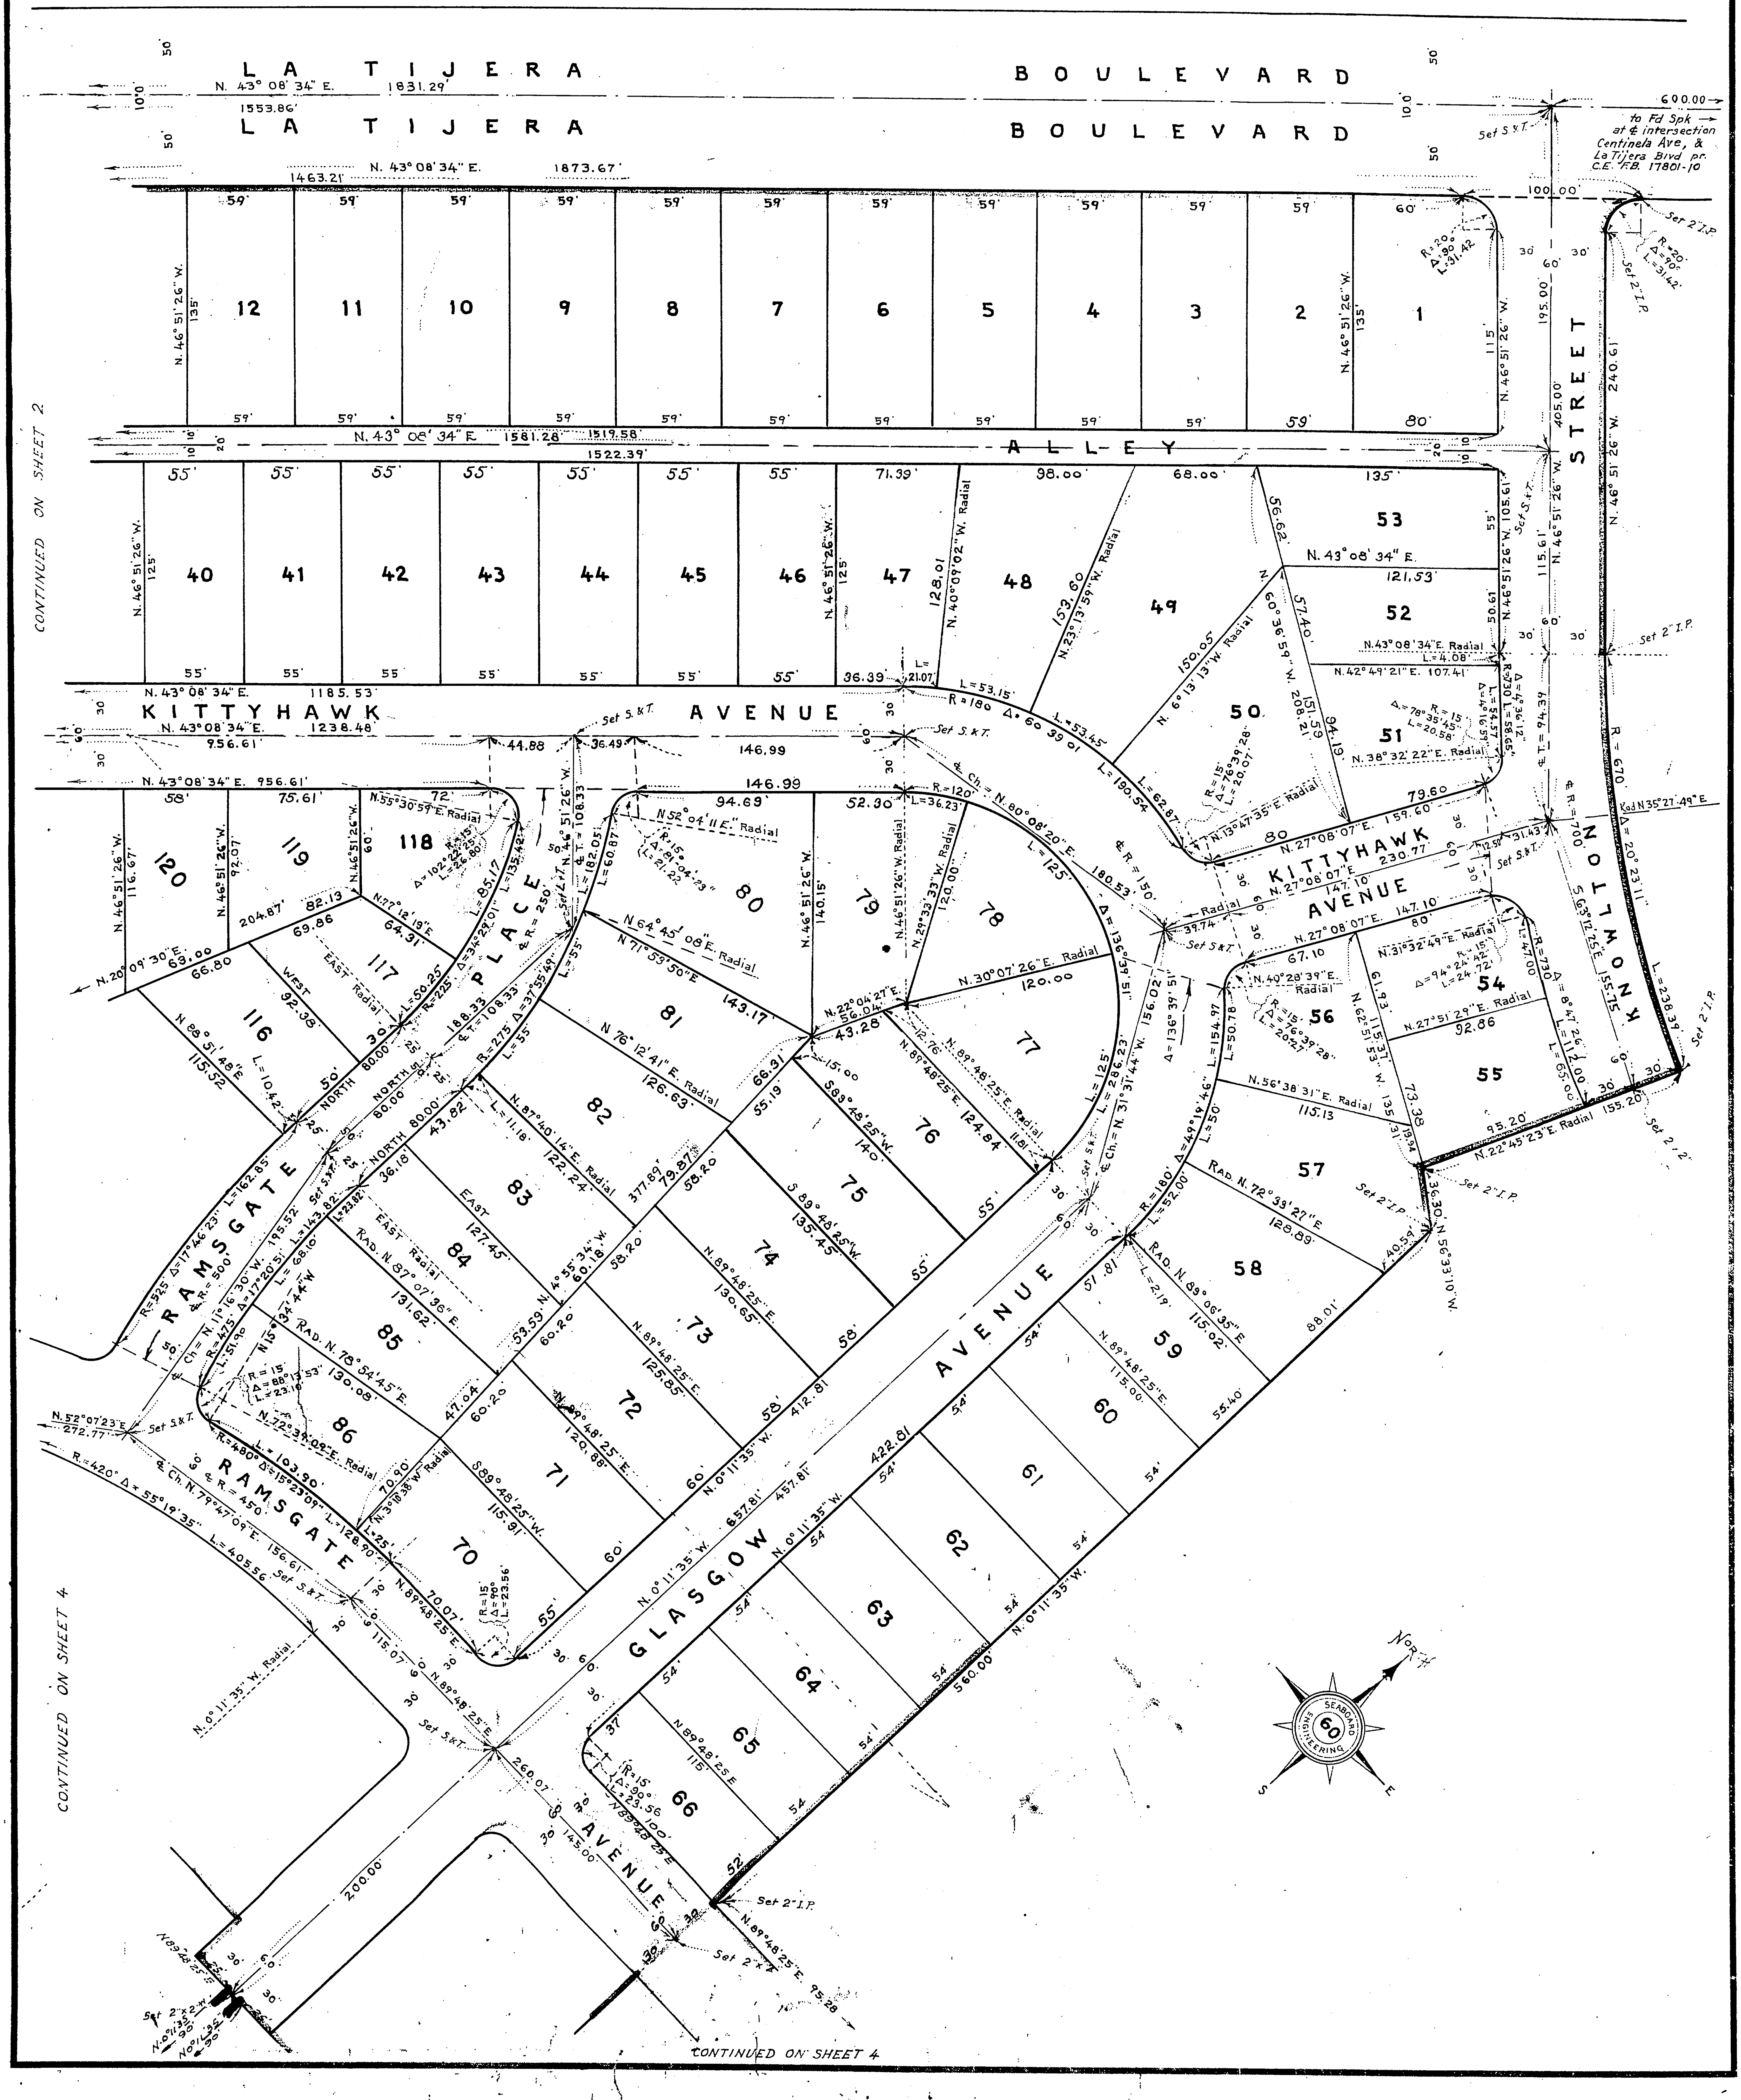

SCALE: 1" = 60'

SHEET 4 OF FOUR SHEETS

TRACT No. 11569

RECORDED

May 22 1947

31 2 P.M.

303

20

Woodbury

Free