354-34

SCALE- 1"= 60'

SHEET 1 OF THREE SHEETS

TRACT NO. 16180

IN THE CITY OF LOS ANGELES,

BEING A SUBDIVISION OF A PORTION OF LOTS 616 AND 617, SHEET 10, TRACT NO. 1000 AS PER MAP RECORDED IN BOOK 19, PAGE 10 OF MAPS. RECORDS OF LOS ANGELES COUNTY.

RECORDED
Sept. 29, 1949
15 [illegible] 3 P.M.
354
34

ENGINEERING SERVICE CORPORATION

Grace L. Bovard
$5.00

BASIS OF BEARINGS

THE BEARING (NORTH) OF THE CENTER LINE OF LOUISE AVENUE AS SHOWN ON MAP OF TRACT NO. 15634, RECORDED IN BOOK 350, PAGES 26 TO 30 INCLUSIVE, RECORDS OF LOS ANGELES COUNTY, CALIFORNIA WAS TAKEN AS THE BASIS OF BEARINGS SHOWN ON THIS MAP.

We hereby certify that we are the owners of or are interested in the land included within the subdivision shown on the annexed map, and that we are the only persons whose consent is necessary to pass a clear title to said land, and we consent to the making and recordation of said map and subdivision as shown within the colored border lines, and hereby dedicate to the public use the Streets, Avenues, Walks and Alleys shown on said map within said subdivision. We also grant and dedicate to the City of Los Angeles the easements for public utility purposes over the strips of land so designated thereon.

SHERMAN PARK DEVELOPMENT CO.

PRESIDENT

Dorothy Twitchell SECRETARY

TITLE INSURANCE AND TRUST COMPANY.
Easement Holder-per
Deed Recorded in Book 6399, page 320
of Deeds

VICE President.

ASSIST. Secretary.

State of California
County of Los Angeles } SS

On this 26th day of SEPTEMBER, 1949, before me EDNA DEWHURST a Notary Public in and for said County, personally appeared E. H. BOOTH, JR. known to me to be the VICE- President, and J. A. WILLETT known to me to be the ASS'T Secretary of Title Insurance and Trust Company, the Corporation that executed the within instrument and known to me to be the persons who executed the within instrument on behalf of the Corporation therein named, and acknowledged that such Corporation executed the same as easement holder.

Edna Dewhurst
Notary Public.
My Commission expires MARCH 1, 1953.

I, J.R. Newville, hereby certify that I am a registered Civil Engineer of the State of California, and that this map consisting of three sheets, correctly represents a survey made under my supervision August, 1949, that the survey is true and complete as shown, that the monuments shown hereon actually exist or will be in place not later than July 1, 1950, that their positions and character are correctly shown, and that said monuments are sufficient to enable the survey to be retraced.

J. R. Newville
REGISTERED CIVIL ENGINEER, CERTIFICATE NO. 5335

STATE OF CALIFORNIA
COUNTY OF LOS ANGELES } SS.

On this 21 day of Sept. 1949, before me June E. Augustine a Notary Public in and for said County, personally appeared [illegible] known to me to be the President, and Dorothy Twitchell known to me to be the Secretary of SHERMAN PARK DEVELOPMENT CO., the Corporation that executed the within instrument and known to me to be the persons who executed the within instrument on behalf of the Corporation therein named, and acknowledged that such Corporation executed the same.

J. E. Augustine
NOTARY PUBLIC
My Commission Expires June 4, 1963

I HEREBY CERTIFY THAT THE CITY COUNCIL OF THE CITY OF LOS ANGELES APPROVED THE ATTACHED MAP AND ACCEPTED ON BEHALF OF THE PUBLIC ALL THE STREETS, ROADS, ALLEYS, HIGHWAYS AND EASEMENTS SHOWN ON SAID MAP AND THEREIN OFFERED FOR DEDICATION EXCEPT THOSE STRIPS MARKED "FUTURE STREET" AND "FUTURE ALLEY" PROVIDED THAT NOTHING HEREIN CONTAINED SHALL BE CONSTRUED AS AN ACCEPTANCE OF ANY IMPROVEMENT MADE IN OR UPON ANY STREET, ROAD, ALLEY, HIGHWAY OR EASEMENT SHOWN ON THIS MAP.

Sept. 29- 1949 CITY CLERK WALTER C. PETERSON
By A. Morris
DEPUTY

I HEREBY CERTIFY THAT THERE IS ON FILE IN THE OFFICE OF THE CITY ENGINEER OF THE CITY OF LOS ANGELES COUNTY OF LOS ANGELES, STATE OF CALIFORNIA, A CERTIFICATE MADE BY THE TITLE INSURANCE AND TRUST COMPANY OF SAID CITY, ORDER NO. 3078003 [illegible]
19__ CERTIFYING [illegible]
OF SAID CITY AND [illegible]
Sherman Park Development Co.
Title Insurance and Trust Company
ARE THE ONLY PERSONS [illegible]
FOR THE RECORDATION [illegible]
CITY ENGINEER
DATE SEPT 27 1949

I HEREBY CERTIFY THAT I HAVE EXAMINED THIS MAP AND THAT THE SUBDIVISION AS SHOWN HEREON IS SUBSTANTIALLY THE SAME AS IT APPEARED ON THE TENTATIVE MAP AND ANY APPROVED ALTERATIONS THEREOF: THAT ALL PROVISIONS OF CHAPTER [illegible] STATUTES OF 1943 AS AMENDED, STATE OF CALIFORNIA AND OF ALL LOCAL ORDINANCES APPLICABLE [illegible] EFFECT AT THE TIME OF [illegible] TENTATIVE MAP HAVE BEEN COMPLIED WITH AND I AM SATISFIED THAT THIS MAP IS TECHNICALLY CORRECT.

CITY ENGINEER
DATE SEPT 27 1949

I HEREBY CERTIFY THAT ALL SPECIAL ASSESSMENTS OF WHICH I AM IN CHARGE, TO WHICH THE LAND INCLUDED IN THE WITHIN SUBDIVISION OR ANY PART THEREOF IS SUBJECT AND WHICH MAY BE PAID IN FULL, HAVE BEEN PAID IN FULL.

Director, Bureau of Assessments C. K. STEELE
Date September 23, 1949 Deputy Harold Yardley

I hereby certify that a [illegible] in the sum of $ 1200.00 duly [illegible] of Los Angeles [illegible] as security for the payment of taxes and special assessments [illegible] shown on map of
TRACT N° 16180 [illegible] as required by law.
Harold J. Ostly [illegible] Clerk of the Board [illegible] County of Los Angeles, State of California
Deputy

Approved Sept. 29, 1949
[illegible], County Surveyor
By F. S. Overton Deputy

TRACT Nº 16180
IN THE CITY OF LOS ANGELES

Scale 1" = 60'

Sheet 2 of 3 Sheets

2

Sept. 29, 1949
15 3 P.M.
354
35

Grace L. Borard
Free

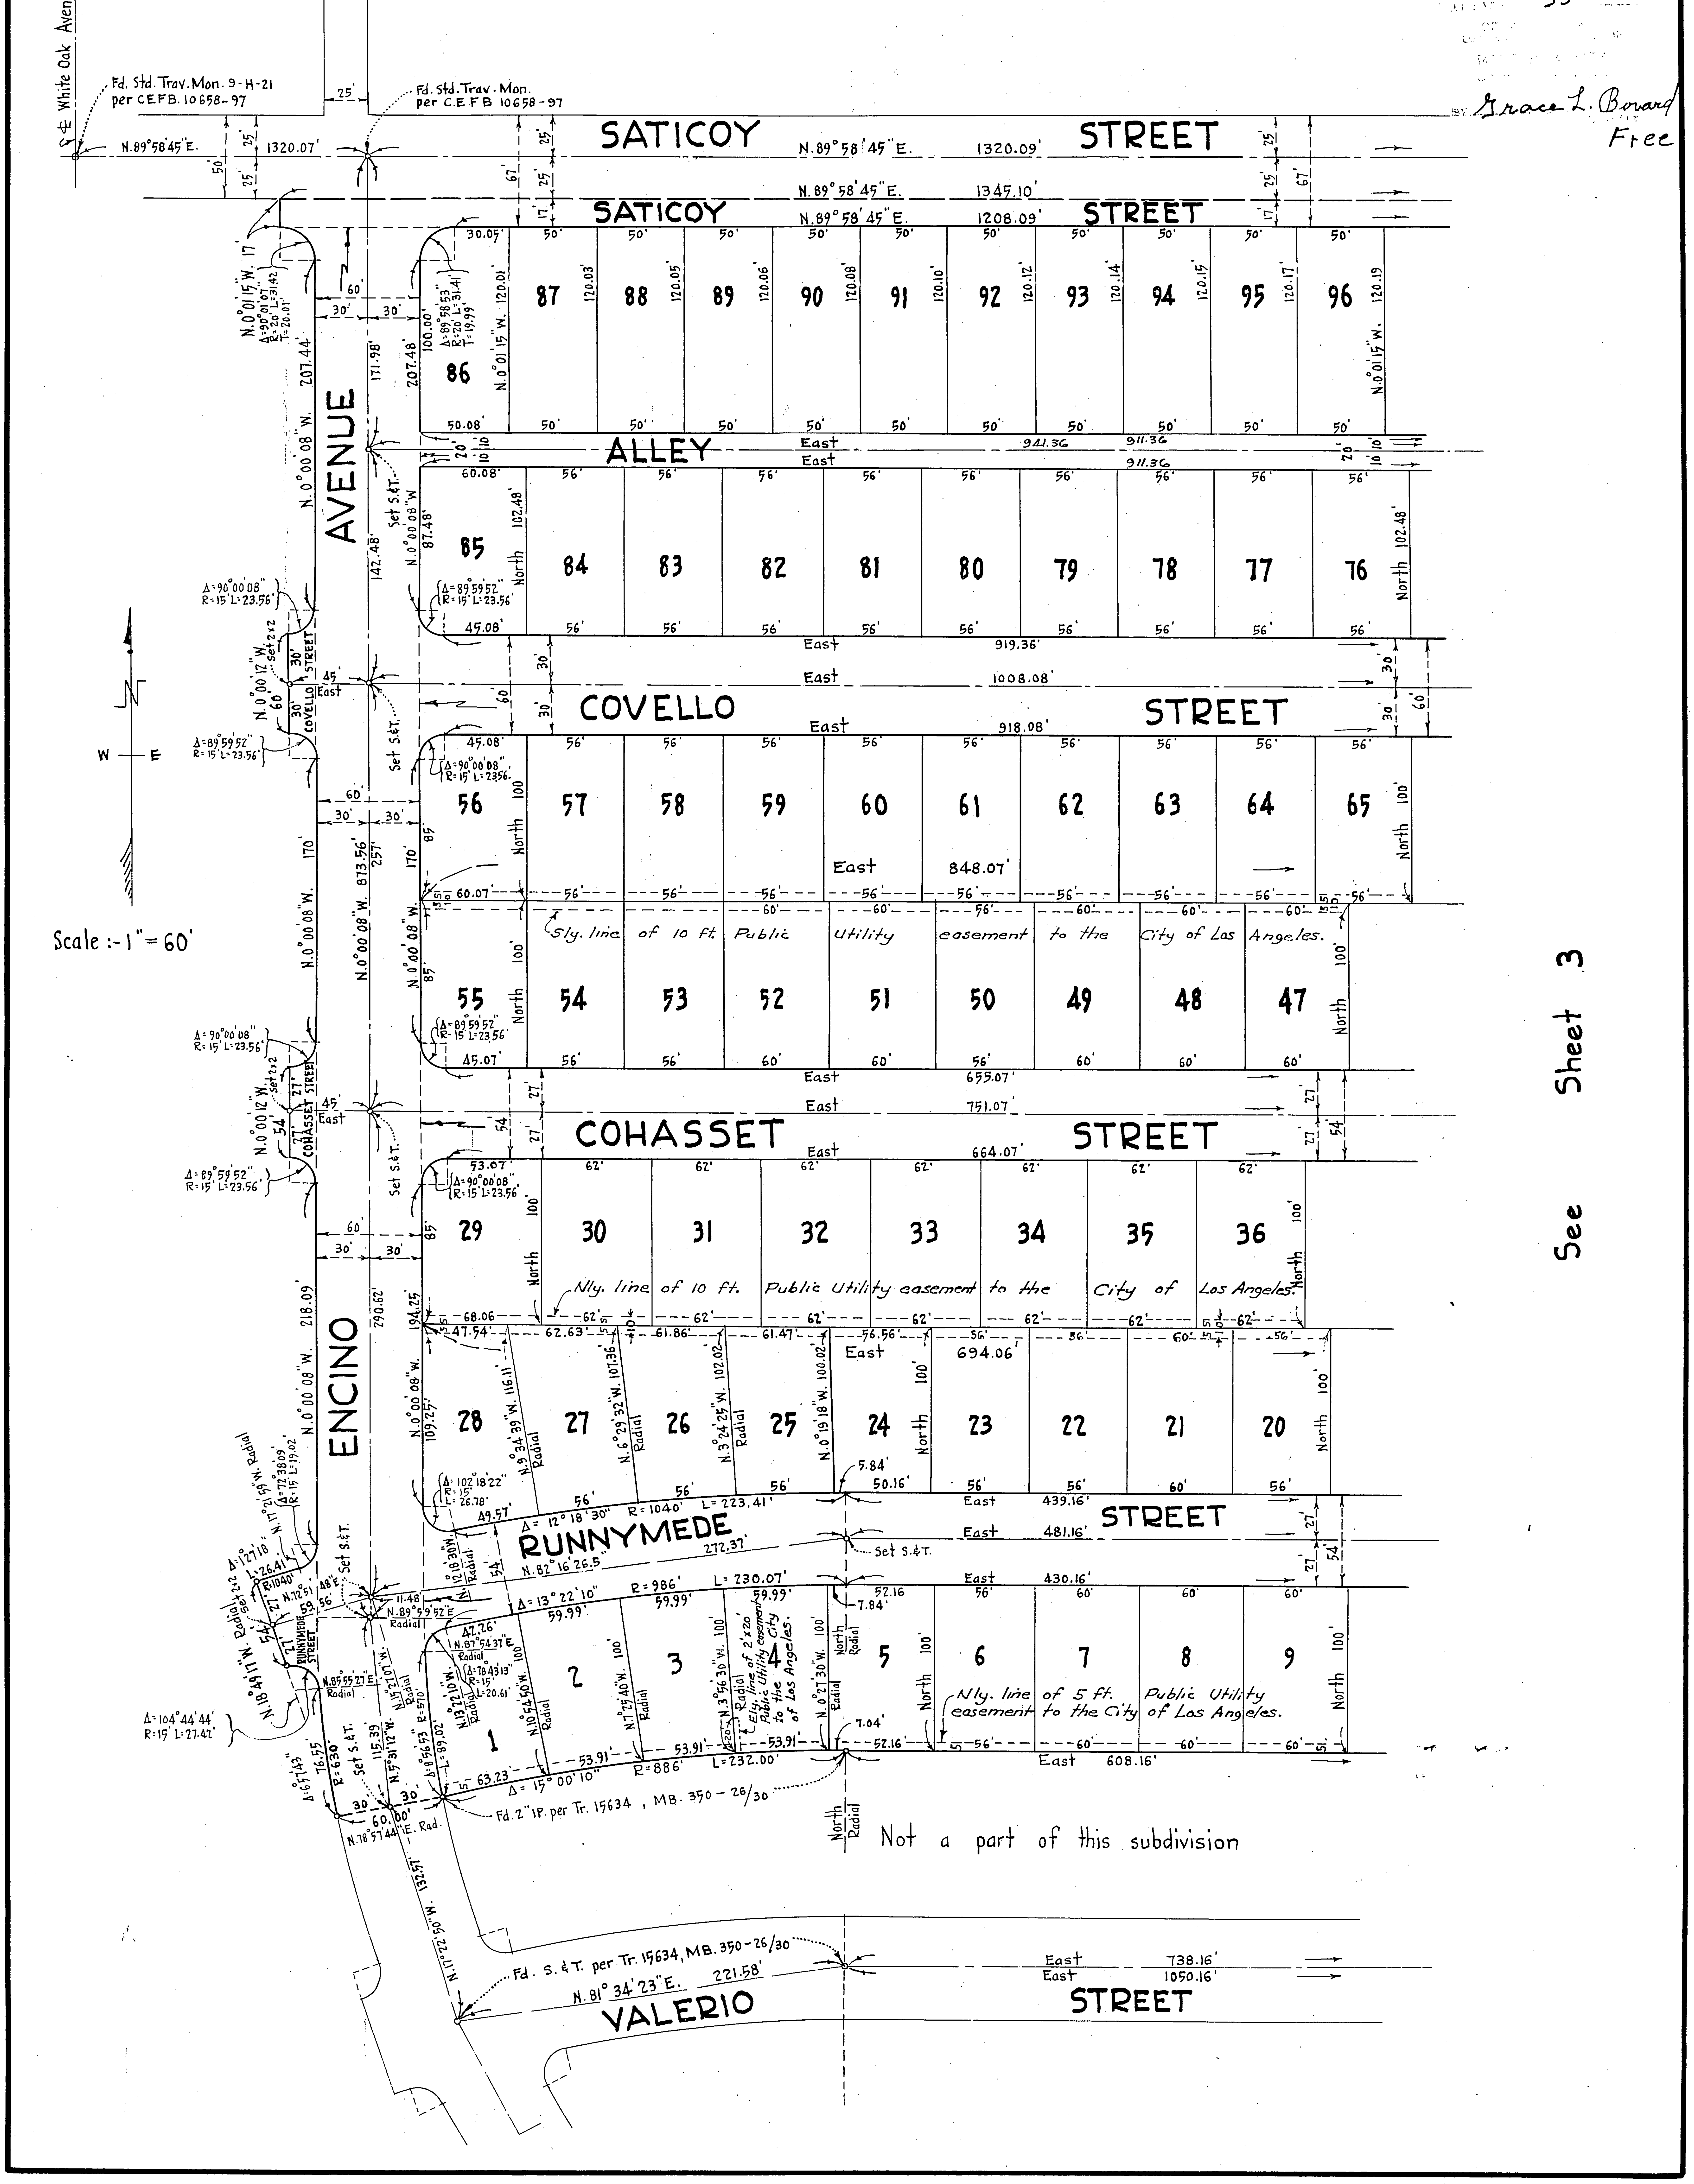

TRACT No. 16180
IN THE CITY OF LOS ANGELES

Sheet 3 of 3 Sheets

RECORDED
Sept. 29 1949
15 3 P.M.
354
36
Grace L. Bovard
Free