TRACT NO. 15254

IN THE CITY OF LOS ANGELES

BEING A SUBDIVISION OF A PORTION OF LOT 606, SHEET 9, TRACT NO. 1000 AS PER MAP RECORDED IN BOOK 19, PAGE 9 OF MAPS IN THE OFFICE OF THE RECORDER OF THE COUNTY OF LOS ANGELES. STATE OF CALIFORNIA

SCALE — 1" = 50'

WM. H. FAIR JR. LICENSED SURVEYOR

RECORDED
AT REQUEST OF OWNER
Mar 22 1950
27 MIN. PAST 4 PM
IN BOOK 369
AT PAGE 31
OF MAP RECORDS
LOS ANGELES COUNTY, CALIF.
MAMIE B. BEATTY
COUNTY RECORDER
BY A G Cungan
#50

We hereby certify that we are the owners of or are interested in the land included within the subdivision shown on the annexed map and we consent to the preparation and recordation of said map and subdivision as shown within the colored border lines, and we hereby dedicate to the public use all Streets, the Avenue and the Alley, shown on said map within said subdivision, and we hereby grant and dedicate to the City of Los Angeles, easements for public utility purposes over the strips of land so designated on said map, and we hereby dedicate for public use for street purposes, Lots 77 and 78 designated as future street on said map within said subdivision, reserving to ourselves for the use of ourselves and successive owners of said Lots, any and all ordinary uses of said lots except the erection or construction of buildings thereon, until such time as the Legislative body shall accept same for street purposes.

I, Wm. H. Fair Jr.; hereby certify that I am a Licensed Surveyor of the State of California; that this map consisting of 3 sheets correctly represents a true and complete survey made under my supervision December, 1949; that the monuments shown hereon actually exist or will be in place not later than July 1st. 1950; that their positions and character are correctly shown, and that said monuments are sufficient to enable the survey to be retraced.

Wm H Fair Jr.
Licensed Surveyor No. 2209.

Title Insurance and Trust Company as Trustee under deeds of Trust, recorded in Book 31949 Pages, 155, 157, 159 and 161 of Official Records.

E. STEINKAMP Inc.

Elwin Steinkamp Jr
President

Vice President

Donna Steinkamp
Secretary.

H. Sheldon
Asst. Secretary.

CITY OF LOS ANGELES

MAYOR

CITY CLERK WALTER C PETERSON

BY A M Morris
DEPUTY

TITLE INSURANCE AND TRUST COMPANY
as easement holder, per Bk. 6399, P. 320, of deeds,

VICE Pres.

H. Sheldon
Asst. Sec.

Hrm

State of California
County of Los Angeles } s.s.

On this 21st day of Mar 1950, before me J J Woodruff a Notary Public in and for said County and State, personally appeared, E H Booth Jr known to me to be the Vice President and H L Sheldon known to me to be the Asst Secretary of The Title Insurance and Trust Company, the corporation that executed the within instrument and known to me to be the persons who executed the within instrument on behalf of the corporation therein named and acknowledged to me that such corporation executed the same.

J J Woodruff
My Commission expires Sept 15 1950 Notary Public

State of California
County of Los Angeles } s.s.

On this 23rd day of February 1950, before me Florence White A Notary Public in and for said County and State, personally appeared Elwain Steinkamp known to me to be the President and Donna Steinkamp known to me to be the Secretary of E. Steinkamp Inc. the corporation that executed the within instrument and known to me to be the persons who executed the within instrument on behalf of the corporation therein named and acknowledged to me that such corporation executed the same.

Florence White
My Commission expires. Dec. 12, 1950 Notary Public

STATE OF CALIFORNIA
COUNTY OF LOS ANGELES } SS
ON THIS 21st **DAY OF** March 1950.
BEFORE ME Henry P. Rio A NOTARY PUBLIC IN AND FOR SAID COUNTY, PERSONALLY APPEARED FLETCHER BOWRON KNOWN TO ME TO BE THE MAYOR, AND A. M. MORRIS KNOWN TO ME TO BE THE Deputy CITY CLERK, OF THE CITY OF LOS ANGELES, THE CORPORATION THAT EXECUTED THE WITHIN INSTRUMENT AND KNOWN TO ME TO BE THE PERSONS WHO EXECUTED THE WITHIN INSTRUMENT ON BEHALF OF THE CORPORATION THEREIN NAMED AND ACKNOWLEDGED TO ME THAT SUCH CORPORATION EXECUTED THE SAME.
(SEAL) **SIGNED** Henry P. Rio
NOTARY PUBLIC

I HEREBY CERTIFY THAT I HAVE EXAMINED THIS MAP AND THAT THE SUBDIVISION AS SHOWN HEREON IS SUBSTANTIALLY THE SAME AS IT APPEARED ON THE TENTATIVE MAP AND ANY APPROVED ALTERATIONS THEREOF: THAT ALL PROVISIONS OF CHAPTER 128 STATUTES OF 1943 AS AMENDED STATE OF CALIFORNIA AND OF ALL LOCAL ORDINANCES APPLICABLE AND IN EFFECT AT THE TIME OF THE APPROVAL OF THE TENTATIVE MAP HAVE BEEN COMPLIED WITH AND I AM SATISFIED THAT THIS MAP IS TECHNICALLY CORRECT
CITY ENGINEER Lloyd Aldrich
DATE MARCH 15 1950

I HEREBY CERTIFY THAT THE CITY COUNCIL OF THE CITY OF LOS ANGELES APPROVED THE ATTACHED MAP AND ACCEPTED ON BEHALF OF THE PUBLIC ALL THE STREETS ROADS, ALLEYS, HIGHWAYS AND EASEMENTS SHOWN ON SAID MAP AND THEREIN OFFERED FOR DEDICATION EXCEPT THOSE STRIPS MARKED "FUTURE STREET" AND "FUTURE ALLEY" PROVIDED THAT NOTHING HEREIN CONTAINED SHALL BE CONSTRUED AS AN ACCEPTANCE OF ANY IMPROVEMENTS MADE IN OR UPON ANY STREET, ROAD, ALLEY, HIGHWAY OR EASEMENT SHOWN ON THIS MAP.
Mar. 17 1950 CITY CLERK WALTER C PETERSON
By A M Morris
DEPUTY

I HEREBY CERTIFY THAT THERE IS ON FILE IN THE OFFICE OF THE CITY ENGINEER OF THE CITY OF LOS ANGELES COUNTY OF LOS ANGELES, STATE OF CALIFORNIA, A CERTIFICATE MADE BY THE TITLE INSURANCE AND TRUST COMPANY OF SAID CITY, ORDER NO. 2891865 DATED MARCH 7 1950 CERTIFYING THAT IT APPEARS FROM THE RECORDS OF SAID CITY AND COUNTY THAT
E. Steinkamp, Inc.
City of Los Angeles
Title Insurance and Trust Company
~~(IS)~~ (ARE) THE ONLY PERSONS WHOSE CONSENT IS REQUIRED FOR THE RECORDING OF THIS MAP BY LAW.
CITY ENGINEER Lloyd Aldrich
DATE MARCH 15 1950

I HEREBY CERTIFY THAT ALL SPECIAL ASSESSMENTS OF WHICH I AM IN CHARGE, TO WHICH THE LAND INCLUDED IN THE WITHIN SUBDIVISION OR ANY PART THEREOF IS SUBJECT AND WHICH MAY BE PAID IN FULL, HAVE BEEN PAID IN FULL.
Director, Bureau of Assessments C. K. STEELE
Date March 6, 1950 Deputy

I hereby certify that a good and sufficient bond in the sum of $675.00 duly approved by the Board of Supervisors of the County of Los Angeles, has been filed with said Board as security for the payment of taxes and special assessments collected as taxes on land shown on map of TRACT No. 15254 as required by law.
Harold J. Ostly, County Clerk and Ex-officio Clerk of the Board of Supervisors of the County of Los Angeles, State of California.
By Inez Johnson Deputy

State of California
County of Los Angeles } s. s.

On this 8th day of Mar 1950, before me J. J. Woodruff a Notary Public in and for said County, personally appeared Case Bradford known to me to me to be the Vice President and H. L. Sheldon known to me to be the Asst. Secretary of the Title Insurance and Trust Company, the corporation that executed the within instrument and known to me to be the persons who executed the within instrument on behalf of the corporation therein named and acknowledged to me that such corporation executed the same. As Trustee

J J Woodruff
My Commission expires Sept. 15 1950 Notary Public

Approved March 22, 1950
C. E. ARNOLD, County Surveyor
By F. S. Overton
Deputy

SHEET 2 OF 3 SHEETS

TRACT NO. 15254

IN THE CITY OF LOS ANGELES

SCALE 1"=50'

WM. H. FAIR JR. LICENSED SURVEYOR

Mar 22 1950
27 4PM
369
32
A.G. Gray
Fee

Basis of Bearing:
The bearing, North, of Louise Avenue formerly Kearney Avenue as shown on a map of Sheet 9, Tract No. 1000, M.B. 19 P. 9, was used as the basis of bearings shown on this map.

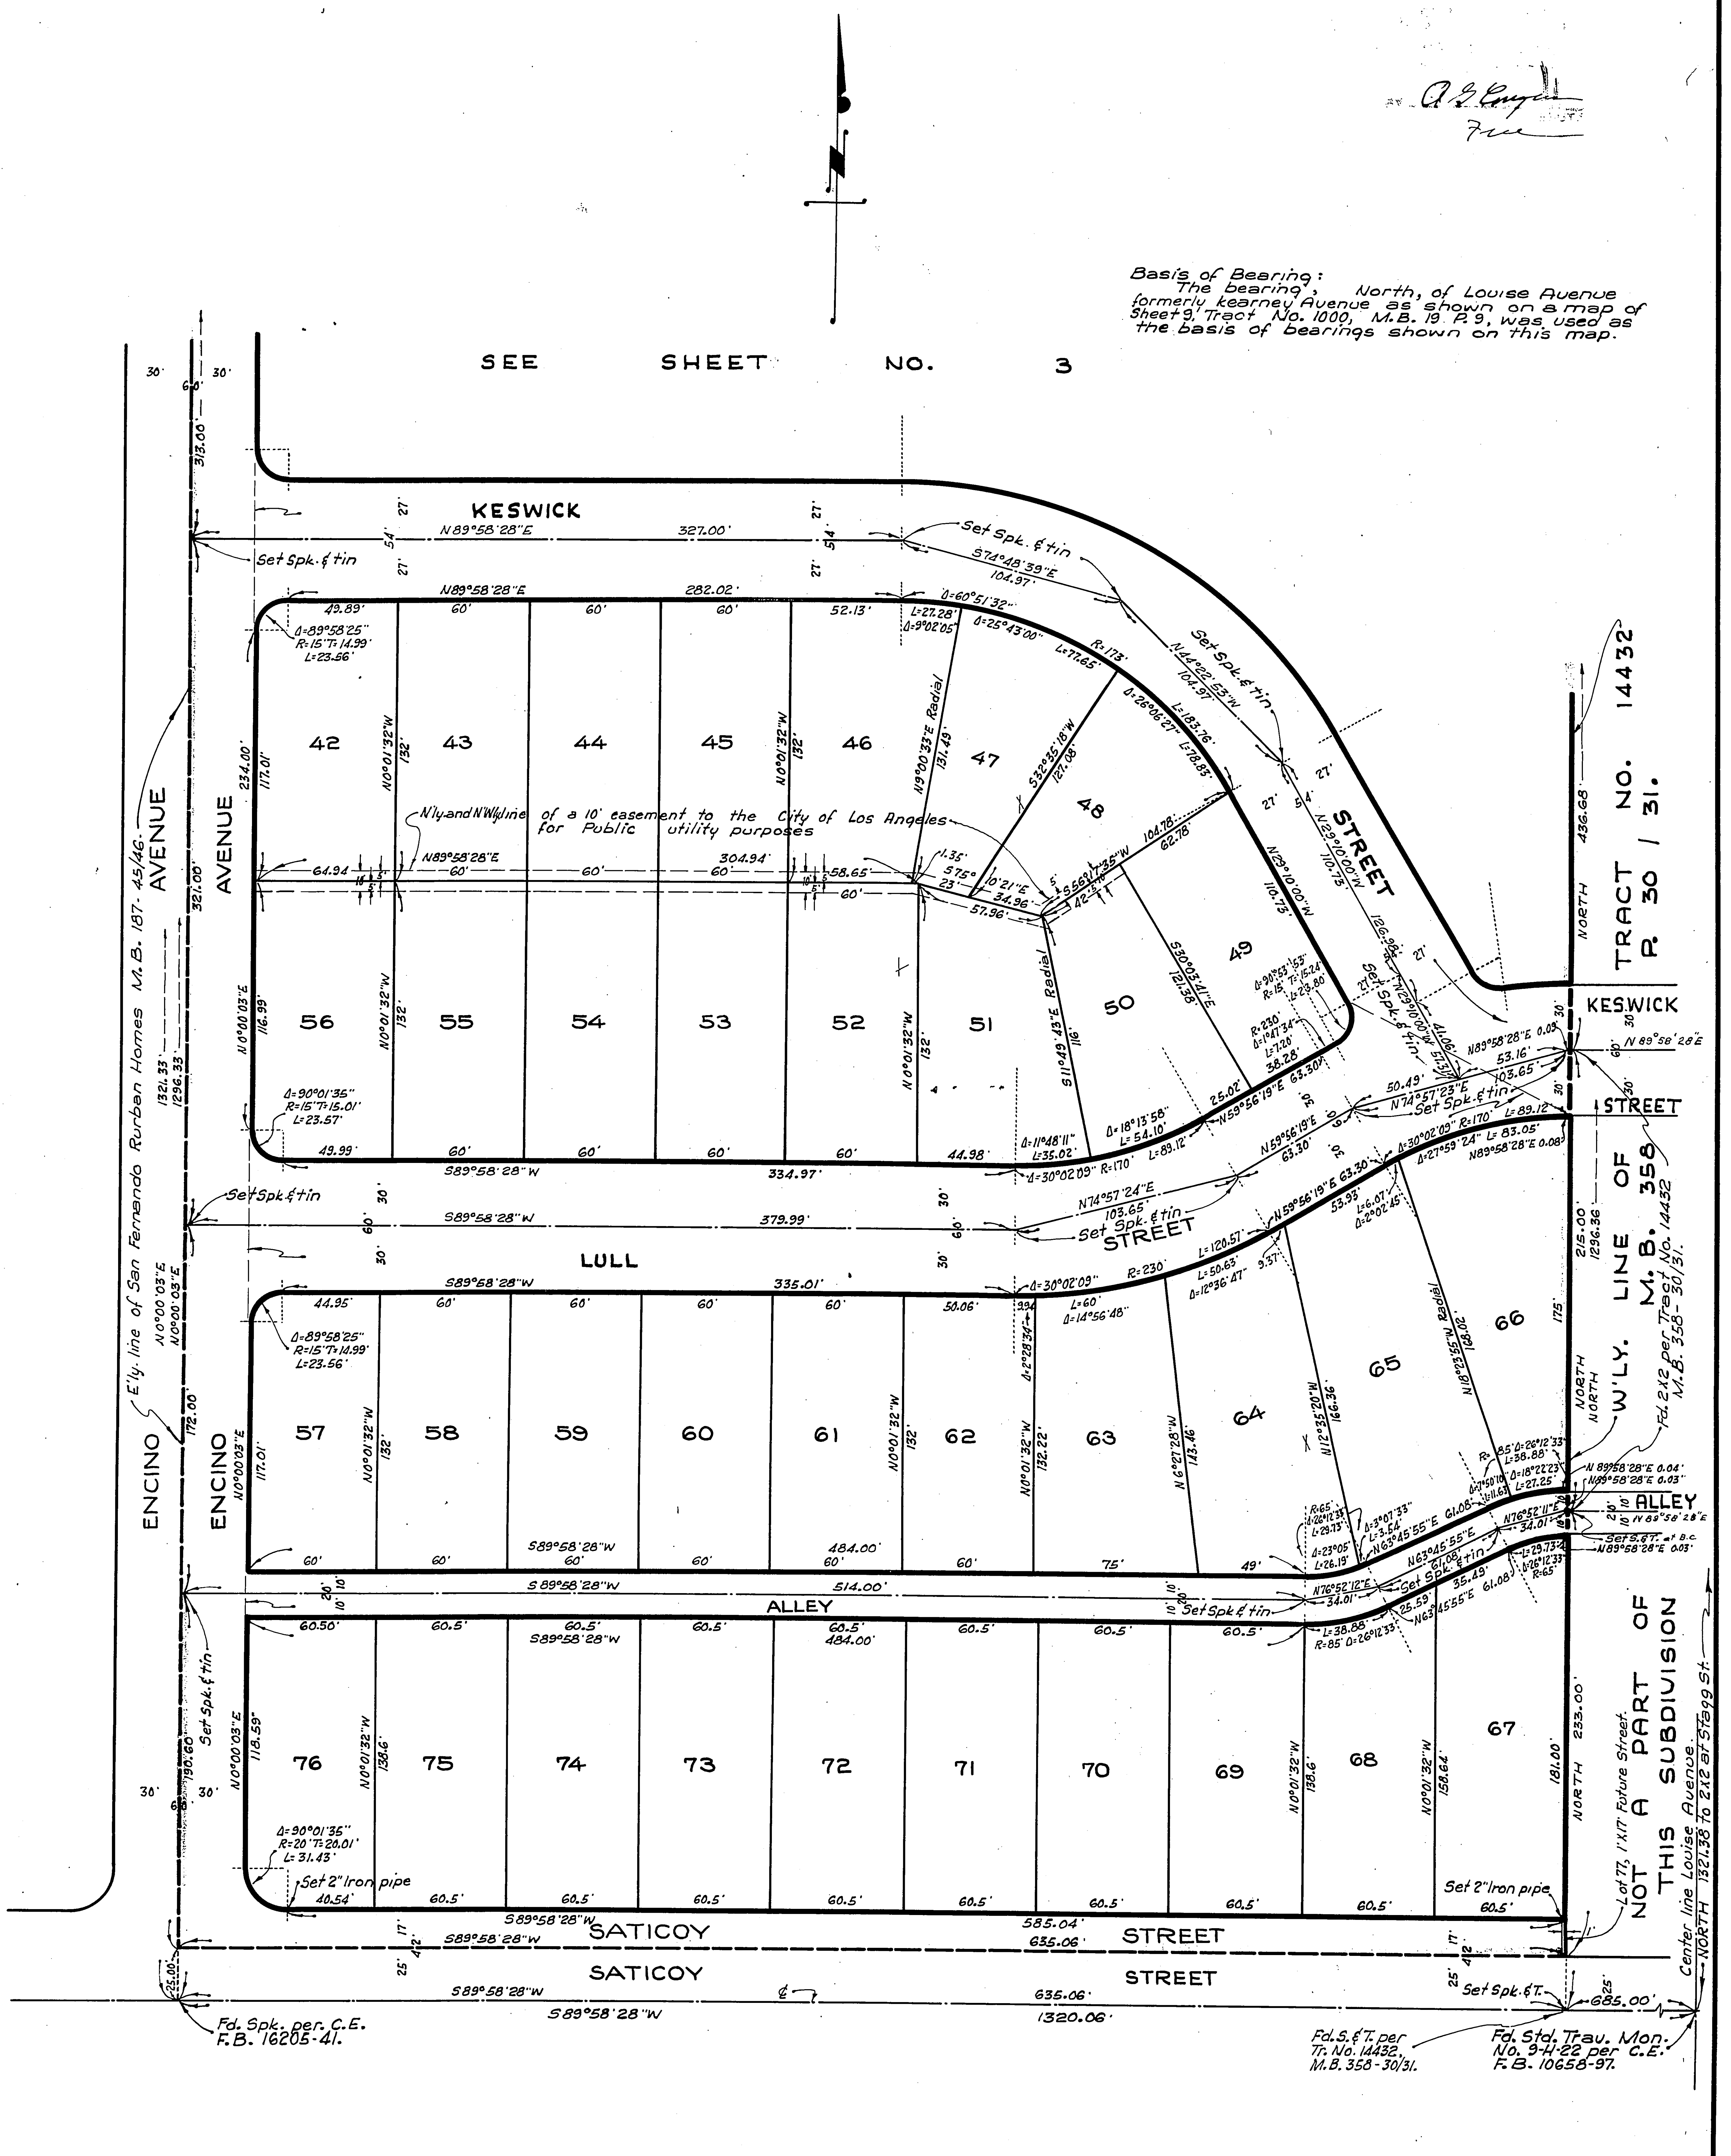

SHEET 3 OF 3 SHEETS

TRACT NO. 15254

IN THE CITY OF LOS ANGELES

SCALE 1"=50'

WM. H. FAIR, JR. LICENSED SURVEYOR

RECORDED
Mar 22 1950
27 MIN. PAST 4 PM
IN BOOK 369
AT PAGE 33
A.B. Cryan
DEPUTY
Fee

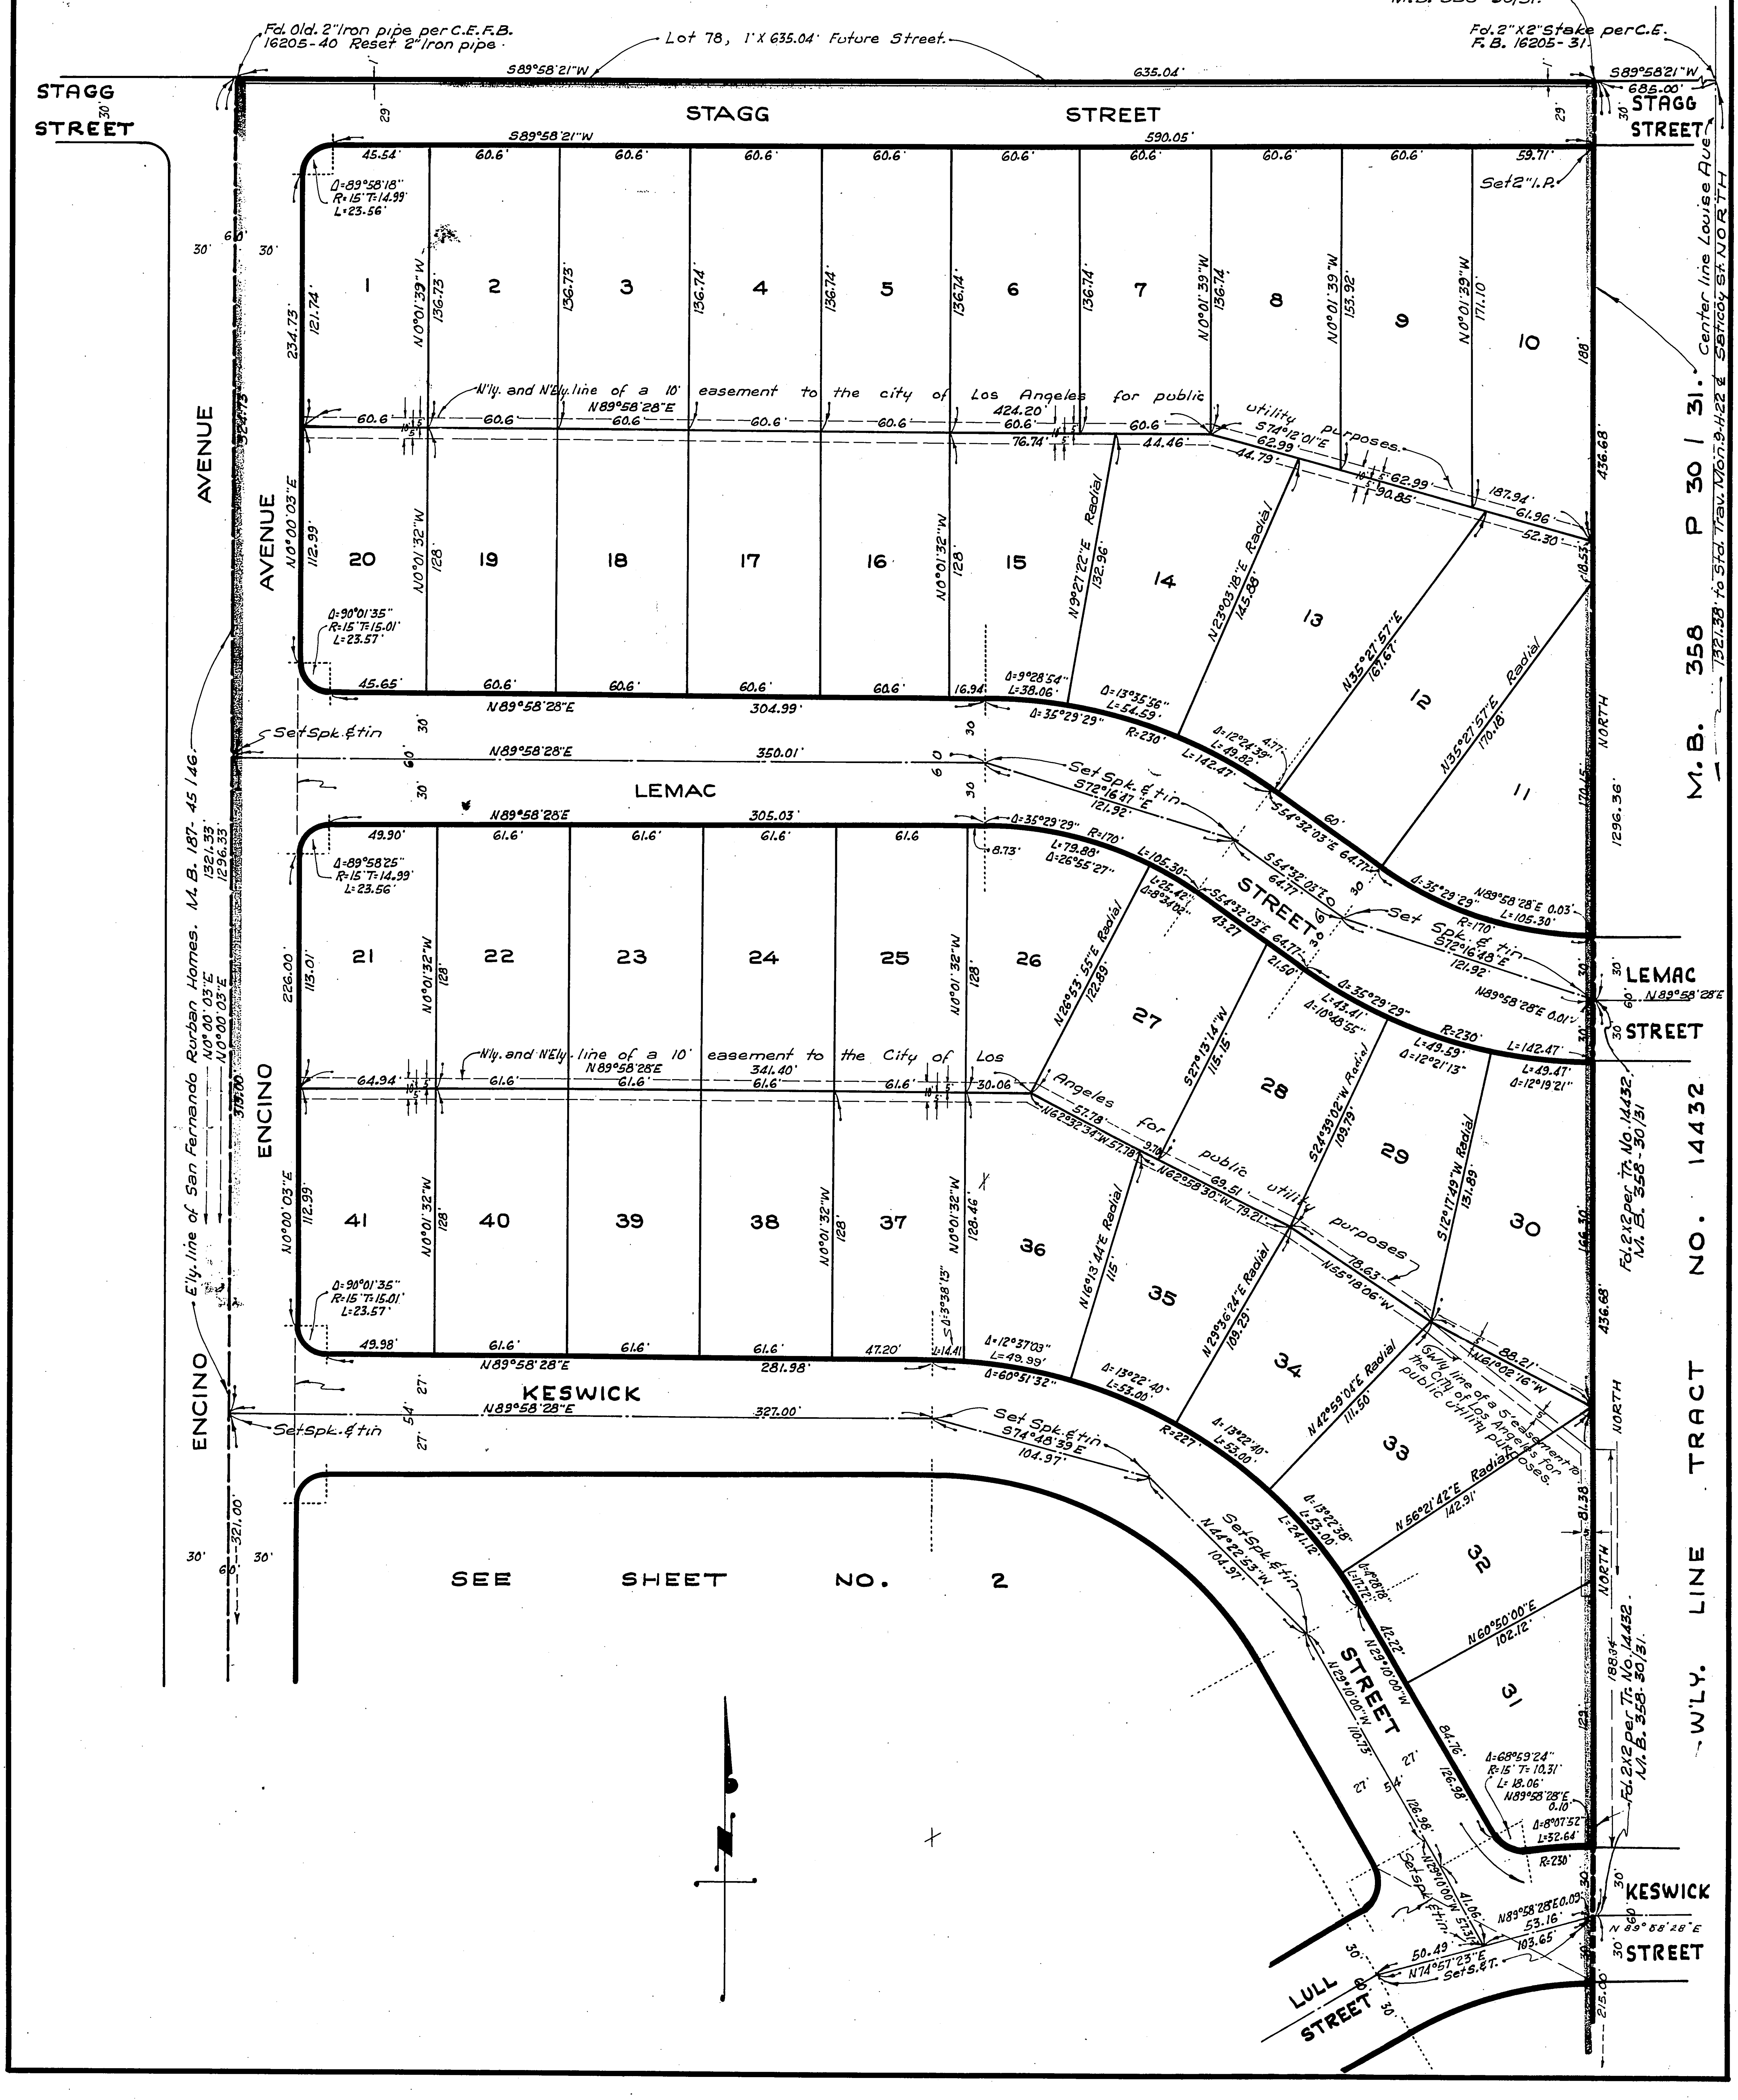
Fd. Old. 2" Iron pipe per C.E.F.B. 16205-40 Reset 2" Iron pipe
Lot 78, 1' X 635.04' Future Street.
Fd. 2" I.P. per Tr. No. 14432. M.B. 358-30/31.
Fd. 2"X2" Stake per C.E. F.B. 16205-31
S89°58'21"W 635.04'
S89°58'21"W 685.00'
STAGG STREET
S89°58'21"W 590.05'
Set 2" I.P.
Δ=89°58'18" R=15' T=14.99' L=23.56'
1
2
3
4
5
6
7
8
9
10
N0°01'39"W
N'ly. and N'Ely. line of a 10' easement to the city of Los Angeles for public utility purposes.
N89°58'28"E 424.20'
S74°12'01"E 62.99'
20
19
18
17
16
15
14
13
12
11
N0°01'32"W
N9°27'22"E Radial
N23°03'18"E Radial
N35°27'57"E
N35°27'57"E Radial
Δ=90°01'35" R=15' T=15.01' L=23.57'
N89°58'28"E 304.99'
Δ=9°28'54" L=38.06'
Δ=13°35'56" L=54.59'
Δ=35°29'29" R=230' L=142.47'
Δ=12°24'39" L=49.82'
Set Spk. & tin
N89°58'28"E 350.01'
LEMAC STREET
Set Spk. & tin S72°16'47"E 121.92'
S54°32'03"E 64.77'
N89°58'28"E 0.03'
R=170' L=105.30'
Set Spk. & tin S72°16'48"E 121.92'
N89°58'28"E 0.01'
N89°58'28"E 305.03'
Δ=35°29'29" R=170' L=79.88' Δ=26°55'27"
Δ=89°58'25" R=15' T=14.99' L=23.56'
21
22
23
24
25
26
27
28
29
30
N26°53'55"E Radial
N27°13'14"W
S24°39'02"W Radial
S12°17'49"W Radial
Δ=35°29'29" R=230' L=142.47'
Δ=12°21'13" L=49.59'
Δ=12°19'21" L=49.47'
N'ly. and N'Ely. line of a 10' easement to the City of Los Angeles for public utility purposes.
N89°58'28"E 341.40'
N62°32'34"W 57.18'
N62°58'30"W 79.21'
N55°18'06"W 78.63'
N61°02'16"W 88.21'
41
40
39
38
37
36
35
34
33
32
31
N16°13'44"E Radial
N29°56'24"E Radial
N42°59'04"E Radial
N56°21'42"E Radial
N60°50'00"E
S'ly. line of a 5' easement to the City of Los Angeles for public utility purposes.
Δ=90°01'35" R=15' T=15.01' L=23.57'
N89°58'28"E 281.98'
Δ=12°37'03" L=49.99'
Δ=60°51'32"
Δ=13°22'40" L=53.00'
R=227'
N89°58'28"E 327.00'
KESWICK STREET
Set Spk. & tin S74°48'39"E 104.97'
Set Spk. & tin N44°22'53"W 104.97'
N29°10'00"W
STREET
Δ=68°59'24" R=15' T=10.31' L=18.06'
Δ=8°07'52" L=32.64'
R=230'
N89°58'28"E 0.10'
N89°58'28"E 0.03'
N74°57'23"E
Set S.&T.
LULL STREET
SEE SHEET NO. 2
ENCINO AVENUE
E'ly. line of San Fernando Rurban Homes. M.B. 187-45/46.
N0°00'03"E
Center line Louise Ave. & Saticoy St. NORTH
M.B. 358 P. 30/31.
1321.38' to Std. Trav. Mon. 9-H22 & Saticoy St.
Fd. 2"x2" per Tr. No. 14432 M.B. 358-30/31.
W'LY. LINE TRACT NO. 14432
NORTH
436.68'
1296.36'