SCALE: 1" = 60'

SHEET 1 OF 5 SHEETS

3736

RECORDED
Dec. 24 1959
48 11 a.m.
651
27

D Walters

13⁰⁰

Tract No. 21892

IN THE CITY OF LOS ANGELES

BEING A SUBDIVISION OF A PORTION OF LOT C RANCHO EL ESCORPION AS PER MAP RECORDED IN BOOK 4232 PAGES 124 AND 125 OF DEEDS, RECORDS OF LOS ANGELES COUNTY, STATE OF CALIFORNIA

SURVEYED BY ENGINEERING SERVICE CORPORATION

The bearing of the Center Line of Platt Avenue (N 2°14'30"E) per map of Tract № 21890 recorded in Book 644 Pages 7 to 14 inclusive of maps, Records of the County of Los Angeles was used as the basis of bearings shown on this map.

ALL 2" IRON PIPES SHOWN HEREON AS SET ARE 6" BELOW SURFACE OF GROUND

We hereby certify that we are the owners of or are interested in the land included within the Subdivision shown on the annexed map and we consent to the preparation and recordation of said map and Subdivision as shown within the colored border lines.

And we hereby dedicate to the public use the streets, highways and other public ways, shown on said map within said Subdivision.

And we hereby grant and dedicate to the City of Los Angeles, easements for public utility purposes over the strips of land so designated on said map.

And we hereby reserve lot 180 for use as a Public Facility until a new Tract Map is approved and recorded over the area of said lot.

And we hereby reserve Lot 179 for use as a church site until a new Tract Map is approved and recorded over the area of said lot.

VALLEYWOOD BUILDING CO.
A LIMITED PARTNERSHIP — OWNER

BY VALLEYWOOD CONSTRUCTION CORP.
A CORPORATION — GENERAL PARTNER

PRESIDENT — SECRETARY

THE EVANGELICAL LUTHERAN CHURCH
A CORPORATION — OWNER

Elmer E. Abrahamson — P. G. Overson
CHAIRMAN OF THE BOARD OF TRUSTEES — SECRETARY OF THE BOARD OF TRUSTEES

Title Insurance and Trust Company
A CORPORATION — TRUSTEE

Under Deed of Trust recorded in Book T-96 page 870 of Official Records

VICE - PRESIDENT — ASS'T - SECRETARY

I HEREBY CERTIFY THAT I AM A REGISTERED CIVIL ENGINEER OF THE STATE OF CALIFORNIA; THAT THIS MAP, CONSISTING OF 5 SHEETS, CORRECTLY REPRESENTS A TRUE AND COMPLETE SURVEY MADE UNDER MY SUPERVISION APRIL 1955; THAT THE MONUMENTS OF THE CHARACTER AND LOCATIONS SHOWN HEREON ARE IN PLACE OR WILL BE IN PLACE WITHIN TWELVE MONTHS FROM THE RECORDING DATE OF THIS MAP; THAT SAID MONUMENTS ARE SUFFICIENT TO ENABLE THE SURVEY TO BE READILY RETRACED AND THAT TIE NOTES TO ALL CENTERLINE MONUMENTS SHOWN HEREON AS SET BY ME WILL BE ON FILE IN THE OFFICE OF THE CITY ENGINEER WITHIN TWELVE MONTHS FROM RECORDING DATE SHOWN HEREON.

REGISTERED CIVIL ENGINEER No. 5335

THE SIGNATURES OF THE PRESENT OWNERS OF ALL OIL, MINERALS, GAS AND OTHER HYDROCARBON SUBSTANCES, AS RESERVED IN THE DEED RECORDED APRIL 7, 1955, IN BOOK 47417, PAGE 214 OFFICIAL RECORDS, HAVE BEEN OMMITTED AS NECESSARY PARTIES TO SIGN THE MAP UNDER THE PROVISIONS OF SECTION 11587 C-(1) OF THE SUBDIVISION MAP ACT, INASMUCH AS SUCH OWNERSHIP DOES NOT INCLUDE A RIGHT OF ENTRY ON THE SURFACE OF THE LAND.

STATE OF CALIFORNIA
COUNTY OF LOS ANGELES } SS.

ON THIS 17th DAY OF September 1959, BEFORE ME S. D. MORAN A NOTARY PUBLIC IN AND FOR SAID COUNTY, PERSONALLY APPEARED R. S. DILLER KNOWN TO ME TO BE THE PRESIDENT, AND IRVING L. KALSMAN KNOWN TO ME TO BE THE SECRETARY OF VALLEYWOOD CONSTRUCTION CORP., THE CORPORATION THAT EXECUTED THE WITHIN INSTRUMENT AS A PARTNER OF VALLEYWOOD BUILDING CO., A LIMITED PARTNERSHIP, AND KNOWN TO ME TO BE THE PERSONS WHO EXECUTED THE WITHININ INSTRUMENT ON BEHALF OF THE CORPORATION THEREIN NAMED AND ACKNOWLEDGED TO ME THAT SUCH CORPORATION EXECUTED THE SAME AS SUCH PARTNER, AND THAT SUCH PARTNER-SHIP EXECUTED THE SAME.

S. D. Moran
S.D. Moran, NOTARY PUBLIC, MY COMMISSION EXPIRES 2-26-61

STATE OF ~~CALIFORNIA~~ Minnesota
COUNTY OF ~~LOS ANGELES~~ Hennepin } SS.

ON THIS 10th DAY OF SEPTEMBER 1959, BEFORE ME A NOTARY PUBLIC IN AND FOR THE COUNTY, PERSONALLY APPEARED ELMER E. ABRAHAMSON KNOWN TO ME TO BE THE CHAIRMAN OF THE BOARD OF TRUSTEES AND T. G. OVERSON KNOWN TO ME TO BE THE SECRETARY OF THE BOARD OF TRUSTEES OF THE EVANGELICAL LUTHERAN CHURCH, THE CORPORATION THAT EXECUTED THE WITHIN INSTRUMENT AND KNOWN TO ME TO BE THE PERSONS WHO EXECUTED THE WITHIN INSTRUMENT ON BEHALF OF THE CORPORATION THEREIN NAMED AND ACKNOWLEDGED TO ME THAT SUCH CORPORATION EXECUTED THE SAME.

LILLIAN E. WILSON — Lillian E. Wilson
NOTARY PUBLIC
MY COMMISSION EXPIRES Jan. 27, 1965

STATE OF CALIFORNIA
COUNTY OF LOS ANGELES } SS.

ON THIS 5th DAY OF OCTOBER 1959, BEFORE ME THE UNDERSIGNED A NOTARY PUBLIC IN AND FOR THE COUNTY, PERSONALLY APPEARED CLAIRE CAHHERT KNOWN TO ME TO BE THE VICE PRESIDENT AND C. J. TIGHE KNOWN TO ME TO BE THE ASS'T SECRETARY OF THE TITLE INSURANCE AND TRUST COMPANY, THE CORPORATION THAT EXECUTED THE WITHIN INSTRUMENT AND KNOWN TO ME TO BE THE PERSONS WHO EXECUTED THE WITHIN INSTRUMENT ON BEHALF OF THE CORPORATION THEREIN NAMED AND ACKNOWLEDGED TO ME THAT SUCH CORPORATION EXECUTED THE SAME AS TRUSTEE.

J. R. Strachan
J. R. STRACHAN, NOTARY PUBLIC
MY COMMISSION EXPIRES 3-9-62

I HEREBY CERTIFY that [illegible] records of the offices of the Bureau of Assessment of the Department of Public Works and the Treasurer of the City of Los Angeles, none of the [illegible] lots or parcels of the subdivision shown on the attached subdivision map will divide any land subject to any special assessment or bond representing a special assessment which may be paid in full, except as follows: None

The amount necessary for the payment in full of such assessment and/or bond at this time is $ None

Date: Dec. 9, 1959

ROBERT C. MACY, Director of the Bureau of Assessment
By
L. V. McCARDLE, Treasurer of the City of Los Angeles
By

I HEREBY CERTIFY that there is on file in the office of the City Engineer of the City of Los Angeles, County of Los Angeles, State of California, a Certificate made by the Title Insurance and Trust Company of said city, Order No. 4356492 dated Dec. 10, 1959, certifying that it appears from the records of said City and County that Valleywood Building Co., The Evangelical Lutheran Church, Title Insurance and Trust Company (are) the only persons whose consent is required for the recording of this map by law.

Lyall A. Pardee
City Engineer Lyall A. Pardee
Date December 15, 1959

Approved December 24, 1959
JOHN A. LAMBIE, County Engineer
By Ralph K. Kennedy
Deputy

I HEREBY CERTIFY that I have examined this map and that the subdivision as shown hereon is substantially the same as it appeared on the tentative map and any approved alterations thereof; that all provisions of chapter 126, statutes of 1943 as amended State of California and of all local ordinances applicable and in effect at the time of the approval of the tentative map have been complied with and I am satisfied that this map is technically correct.

Lyall A. Pardee
City Engineer Lyall A. Pardee
Date December 15, 1959

I HEREBY CERTIFY THAT THE CITY COUNCIL OF THE CITY OF LOS ANGELES APPROVED THE ATTACHED MAP AND ACCEPTED ON BEHALF OF THE PUBLIC ALL THE STREETS, ROADS, ALLEYS, HIGHWAYS AND EASEMENTS SHOWN ON SAID MAP AND THEREIN OFFERED FOR DEDICATION EXCEPT THOSE STRIPS MARKED "FUTURE STREET" AND "FUTURE ALLEY" PROVIDED THAT NOTHING HEREIN CONTAINED SHALL BE CONSTRUED AS AN ACCEPTANCE OF ANY IMPROVEMENTS MADE IN OR UPON ANY STREET, ROAD, ALLEY, HIGHWAY OR EASEMENT SHOWN ON THIS MAP.

December 23, 1959 CITY CLERK Walter C. Peterson

By Albert Orsatti
Deputy

SHEET 2 OF 5 SHEETS

3730

Tract [illegible] 1792

IN THE CITY OF LOS ANGELES

SURVEYED BY ENGINEERING SERVICE CORPORATION

RECORDED Pg 1
AT REQUEST OF OWNER
Dec. 24 1959
48 MIN. PAST 11 a.m.
IN BOOK 651
AT PAGE 28
OF MAP RECORDS
LOS ANGELES COUNTY, CALIF.
RAY E. LEE
COUNTY RECORDER
BY D. Wallis
DEPUTY

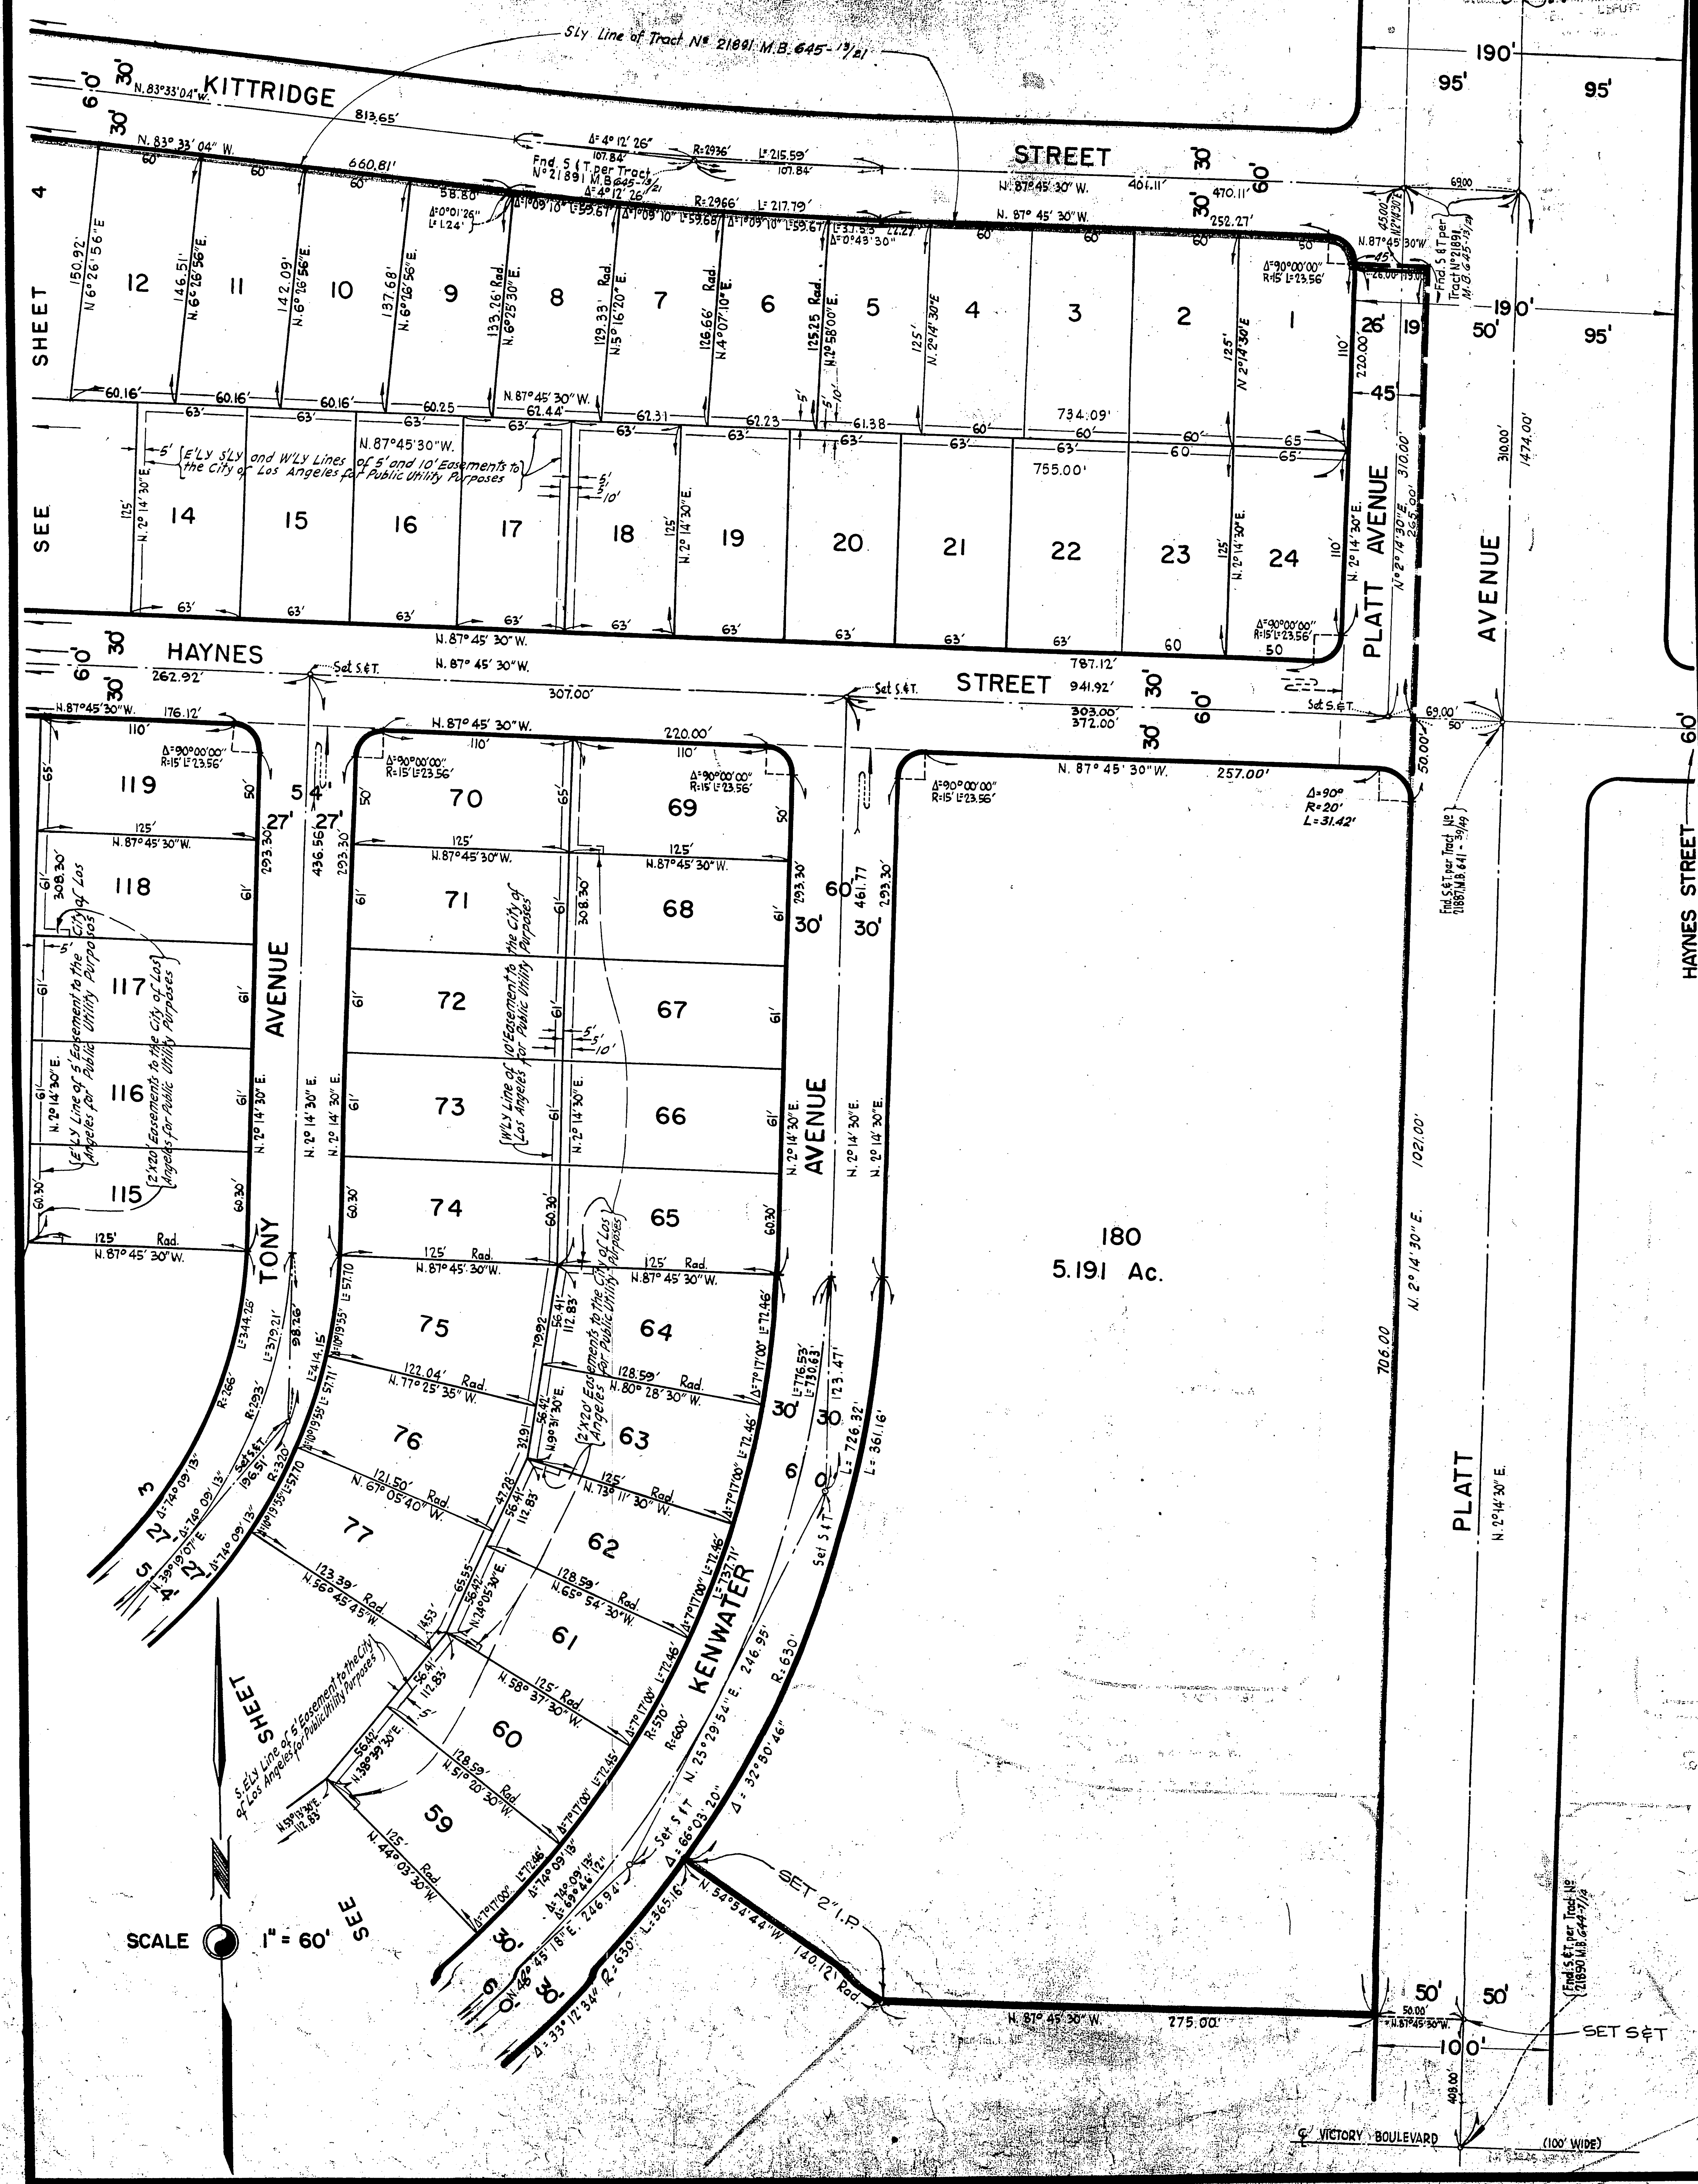
S'Ly Line of Tract Nº 21891 M.B. 645-13/21
KITTRIDGE STREET
N. 83°33'04" W.
813.65'
660.81'
Fnd. S. & T. per Tract Nº 21891 M.B. 645-13/21
N. 87°45'30" W.
401.11'
470.11'
252.27'
190'
95'
95'
12
11
10
9
8
7
6
5
4
3
2
1
14
15
16
17
18
19
20
21
22
23
24
SEE SHEET 4
E'Ly S'Ly and W'Ly Lines of 5' and 10' Easements to the City of Los Angeles for Public Utility Purposes
734.09'
755.00'
PLATT AVENUE
AVENUE
HAYNES STREET
262.92'
307.00'
941.92'
787.12'
303.00'
372.00'
Set S. & T.
119
118
117
116
115
70
71
72
73
74
75
76
77
69
68
67
66
65
64
63
62
61
60
59
180
5.191 Ac.
TONY AVENUE
KENWATER AVENUE
W'Ly Line of 10' Easement to the City of Los Angeles for Public Utility Purposes
E'Ly Line of 5' Easement to the City of Los Angeles for Public Utility Purposes
2'x20' Easements to the City of Los Angeles for Public Utility Purposes
S.E'Ly Line of 5' Easement to the City of Los Angeles for Public Utility Purposes
SEE SHEET 3
SCALE 1" = 60'
SET 2" I.P.
N. 54°54'44" W. 140.12' Rad.
N. 87°45'30" W. 275.00'
PLATT
N. 2°14'30" E.
1021.00'
706.00
Fnd. S. & T. per Tract Nº 21887 M.B. 641-39/49
Fnd. S. & T. per Tract Nº 21650 M.B. 644-1/14
SET S & T
100'
50'
50'
℄ VICTORY BOULEVARD (100' WIDE)
HAYNES STREET
1474.00'
310.00'

SHEET 3 OF 5 SHEETS

3736

Pg2

CORDED

Dec. 24. 1959
48 11 a.m.
651
79

D Walters

Tract No. 21892

IN THE CITY OF LOS ANGELES

SURVEYED BY ENGINEERING SERVICE CORPORATION

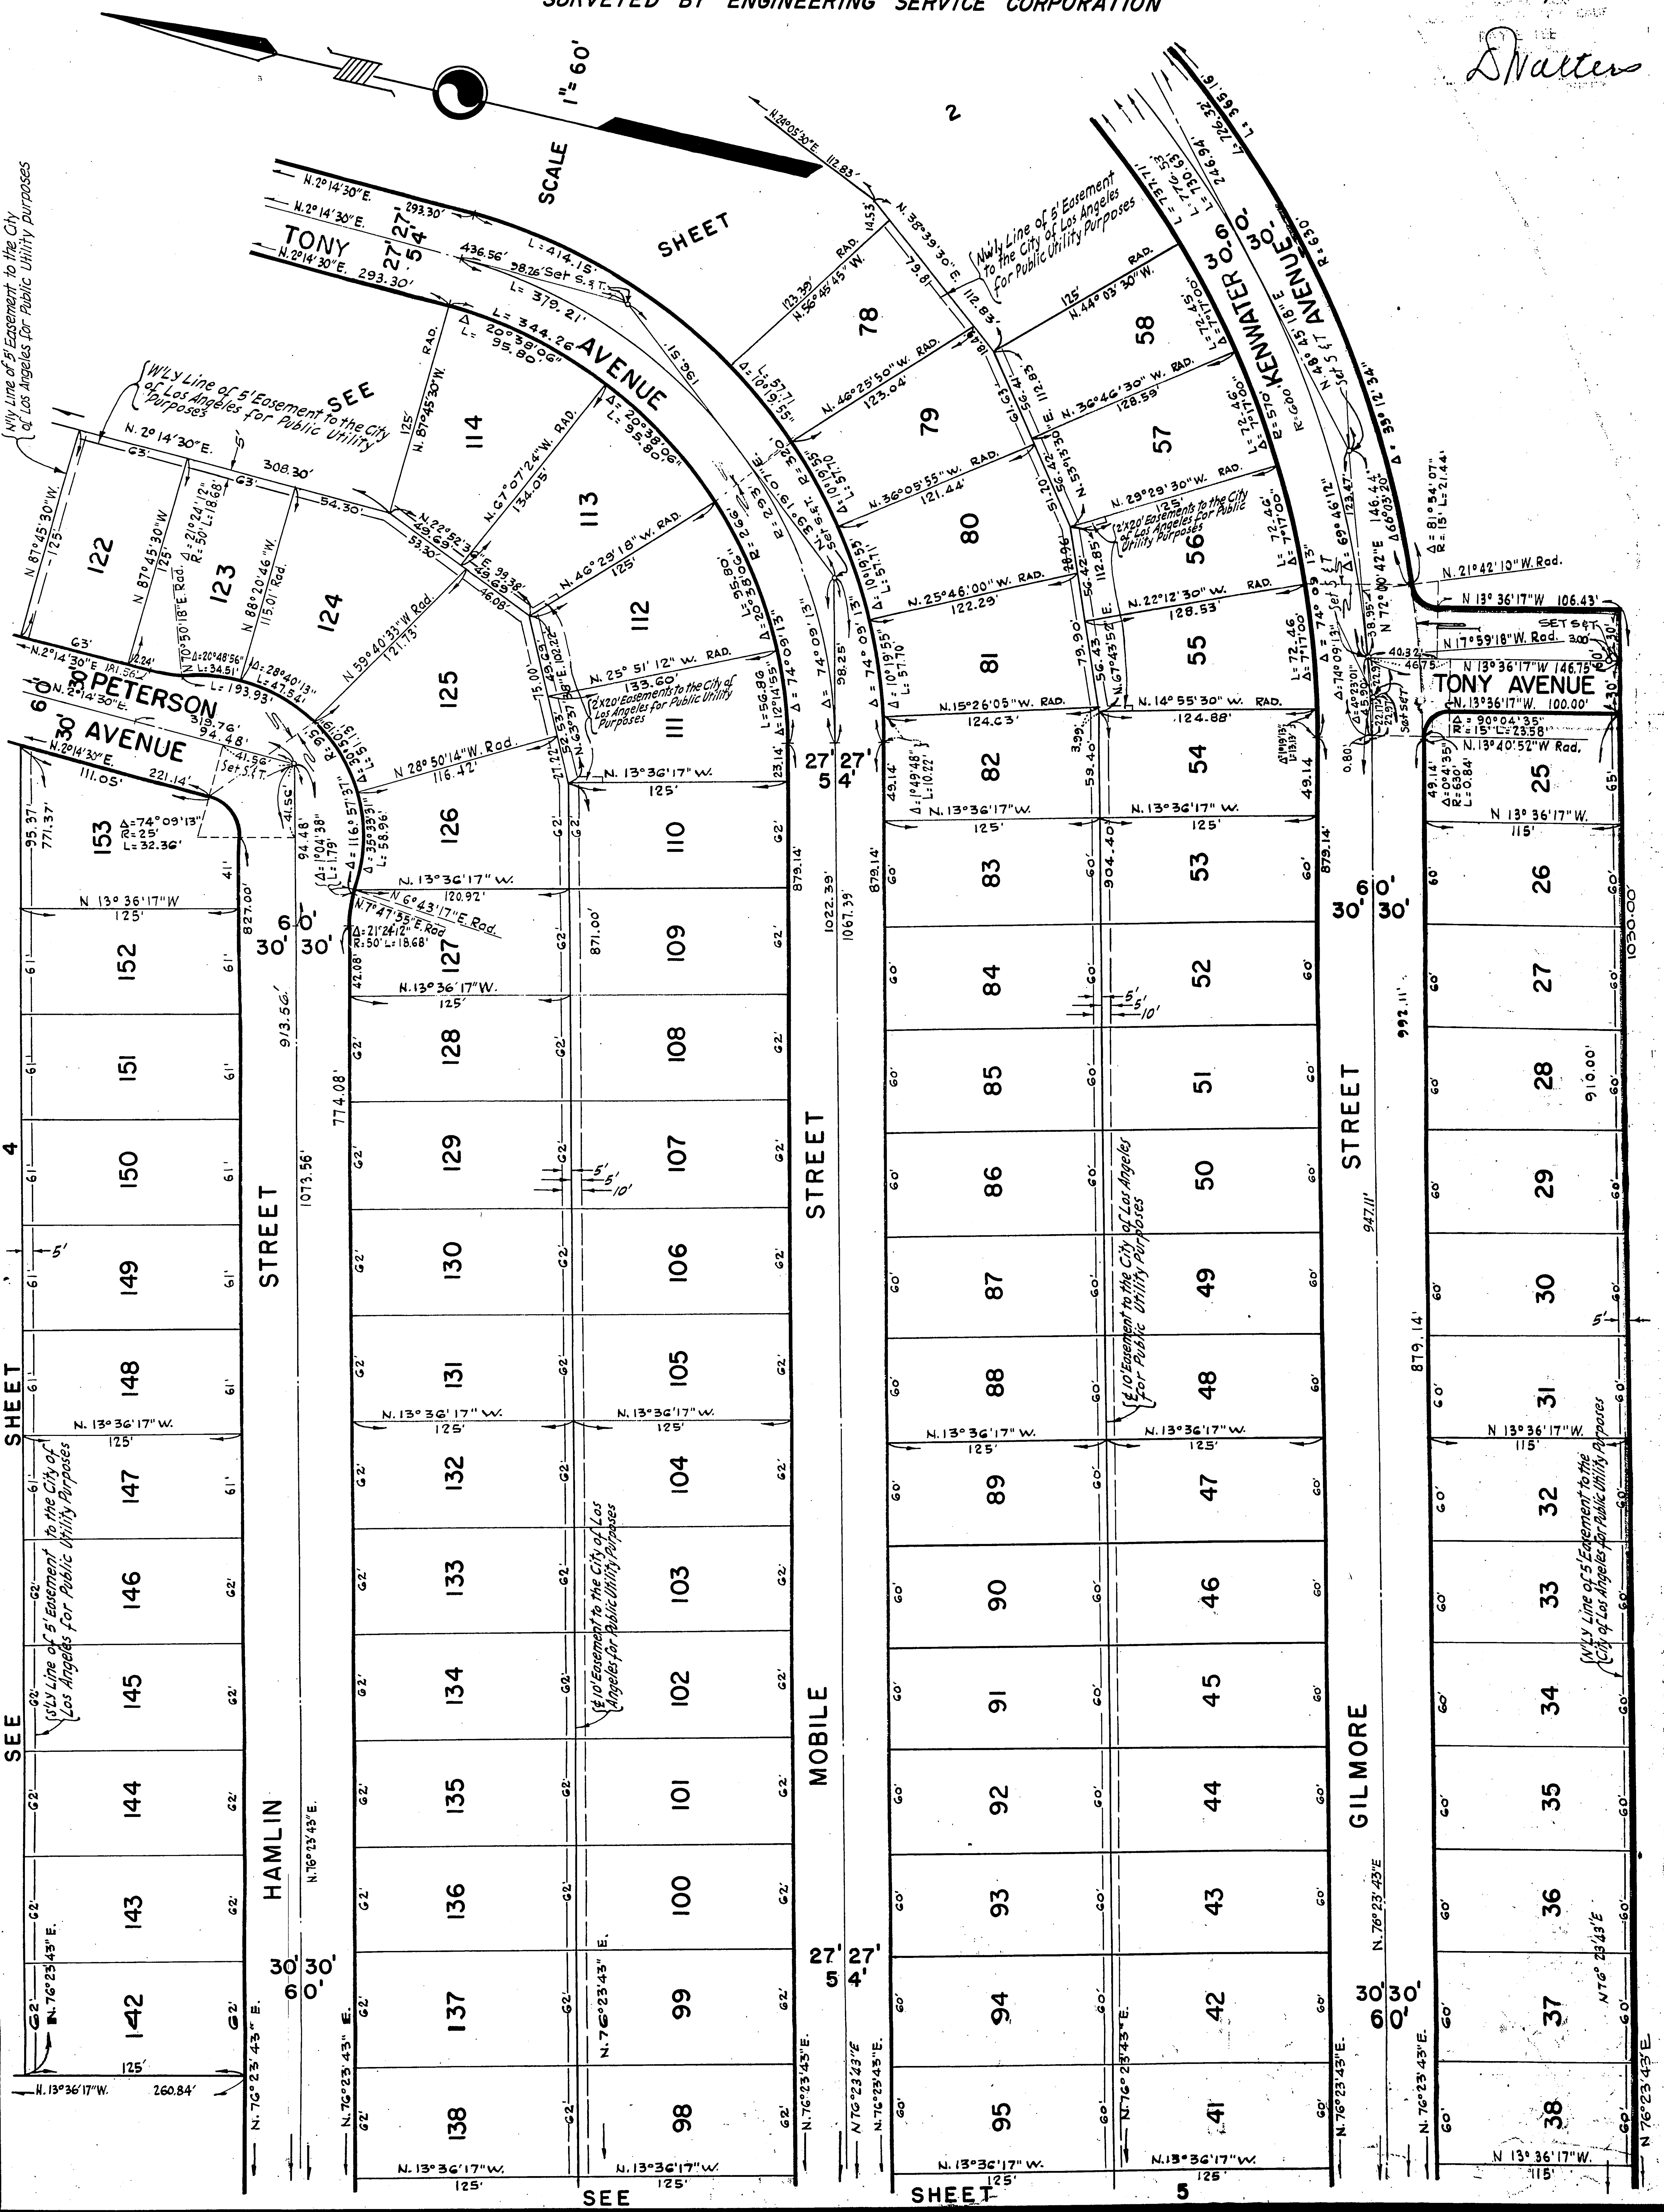

651 30

SHEET 4 OF 5 SHEETS

3736 Pg 4

RECORDED
Dec. 24 1959
48 11 am
651
30

S Walter

Tract No. 21892

IN THE CITY OF LOS ANGELES

SURVEYED BY ENGINEERING SERVICE CORPORATION

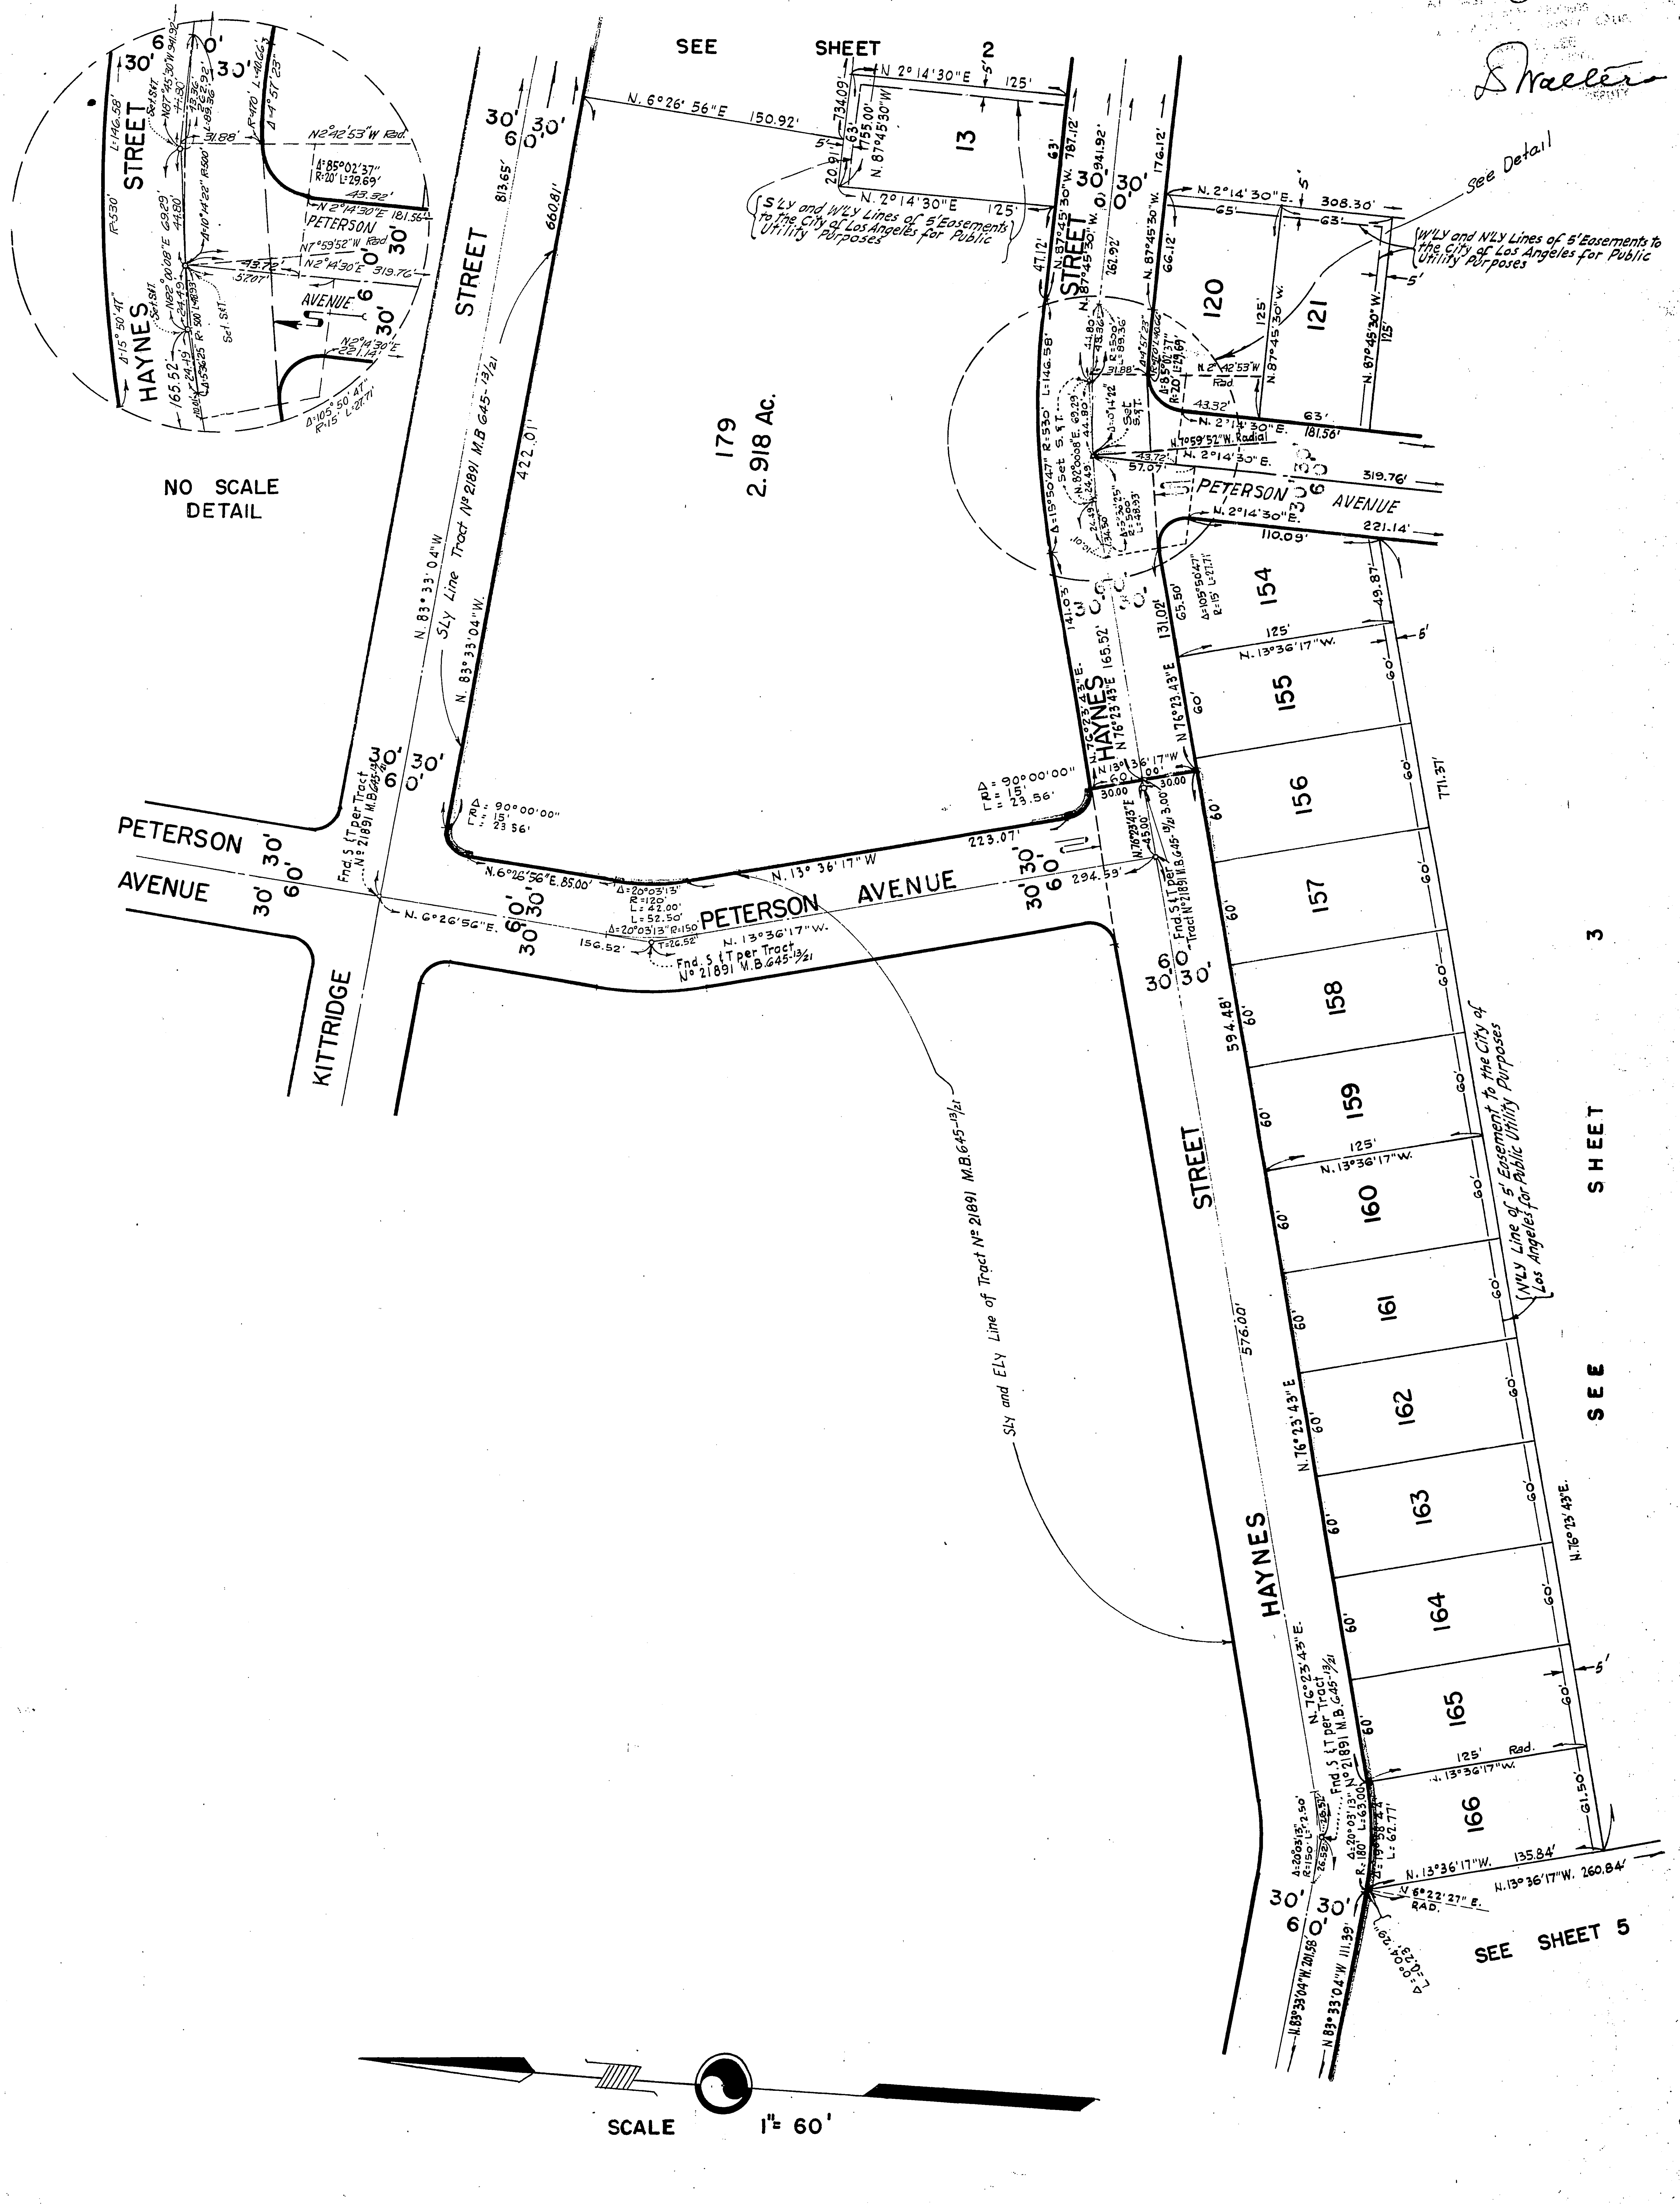
SEE SHEET 2
SEE SHEET 3
SEE SHEET 5
See Detail
NO SCALE DETAIL
HAYNES STREET
PETERSON AVENUE
KITTRIDGE STREET
179
2.918 Ac.
13
120
121
154
155
156
157
158
159
160
161
162
163
164
165
166
S'Ly and W'Ly Lines of 5' Easements to the City of Los Angeles for Public Utility Purposes
W'LY and N'LY Lines of 5' Easements to the City of Los Angeles for Public Utility Purposes
W'LY Line of 5' Easement to the City of Los Angeles for Public Utility Purposes
S'Ly Line Tract Nº 21891 M.B. 645-13/21
S'Ly and E'Ly Line of Tract Nº 21891 M.B. 645-13/21
Fnd. S & T per Tract Nº 21891 M.B. 645-13/21
N. 6°26'56"E 150.92'
N. 2°14'30"E 125'
N. 87°45'30"W 155.00'
N. 83°33'04"W
813.65'
660.81'
422.01'
N. 87°45'30"W 187.12'
N. 87°45'30"W 241.92'
N. 2°14'30"E 308.30'
N. 2°14'30"E 319.76'
221.14'
N. 13°36'17"W 223.07'
294.59'
N. 6°26'56"E 85.00'
N. 76°23'43"E
594.48'
576.00'
N. 13°36'17"W 135.84'
N. 13°36'17"W 260.84'
771.51'
Δ=90°00'00" R=15' L=23.56'
Δ=20°03'13" R=120' L=42.00'
Δ=20°03'13" R=150' L=52.50'
Δ=105°50'47" R=15' L=27.71'
Δ=85°02'37" R=20' L=29.69'
Δ=15°50'47" R=530' L=146.58'
N. 7°59'52"W Radial
N. 2°42'53"W Rad.
N. 6°22'27"E RAD.
SCALE 1" = 60'

SHEET 5 OF 5 SHEETS

3726 P95

Tract No. 21892

IN THE CITY OF LOS ANGELES

SURVEYED BY ENGINEERING SERVICE CORPORATION

Dec. 24 1959
48 11 a m
6 51
31

D Walters